


THIS DRAWING AND THE DESIGN IT COVERS ARE THE PROPERTY OF TENGIZCHEVROIL THEY ARE MERELY LOANED AND ON THE BORROWERS EXPRESS AGREEMENT THAT THEY WILL NOT BE REPRODUCED COPIED LOANED EXHIBITED NOR USED EXCEPT IN THE LIMITED WAY AND PRIVATE USE PERMITTED AND WRITTEN CONSENT GIVEN BY TENGIZCHEVROIL TO THE BORROWER.

L-SK-002

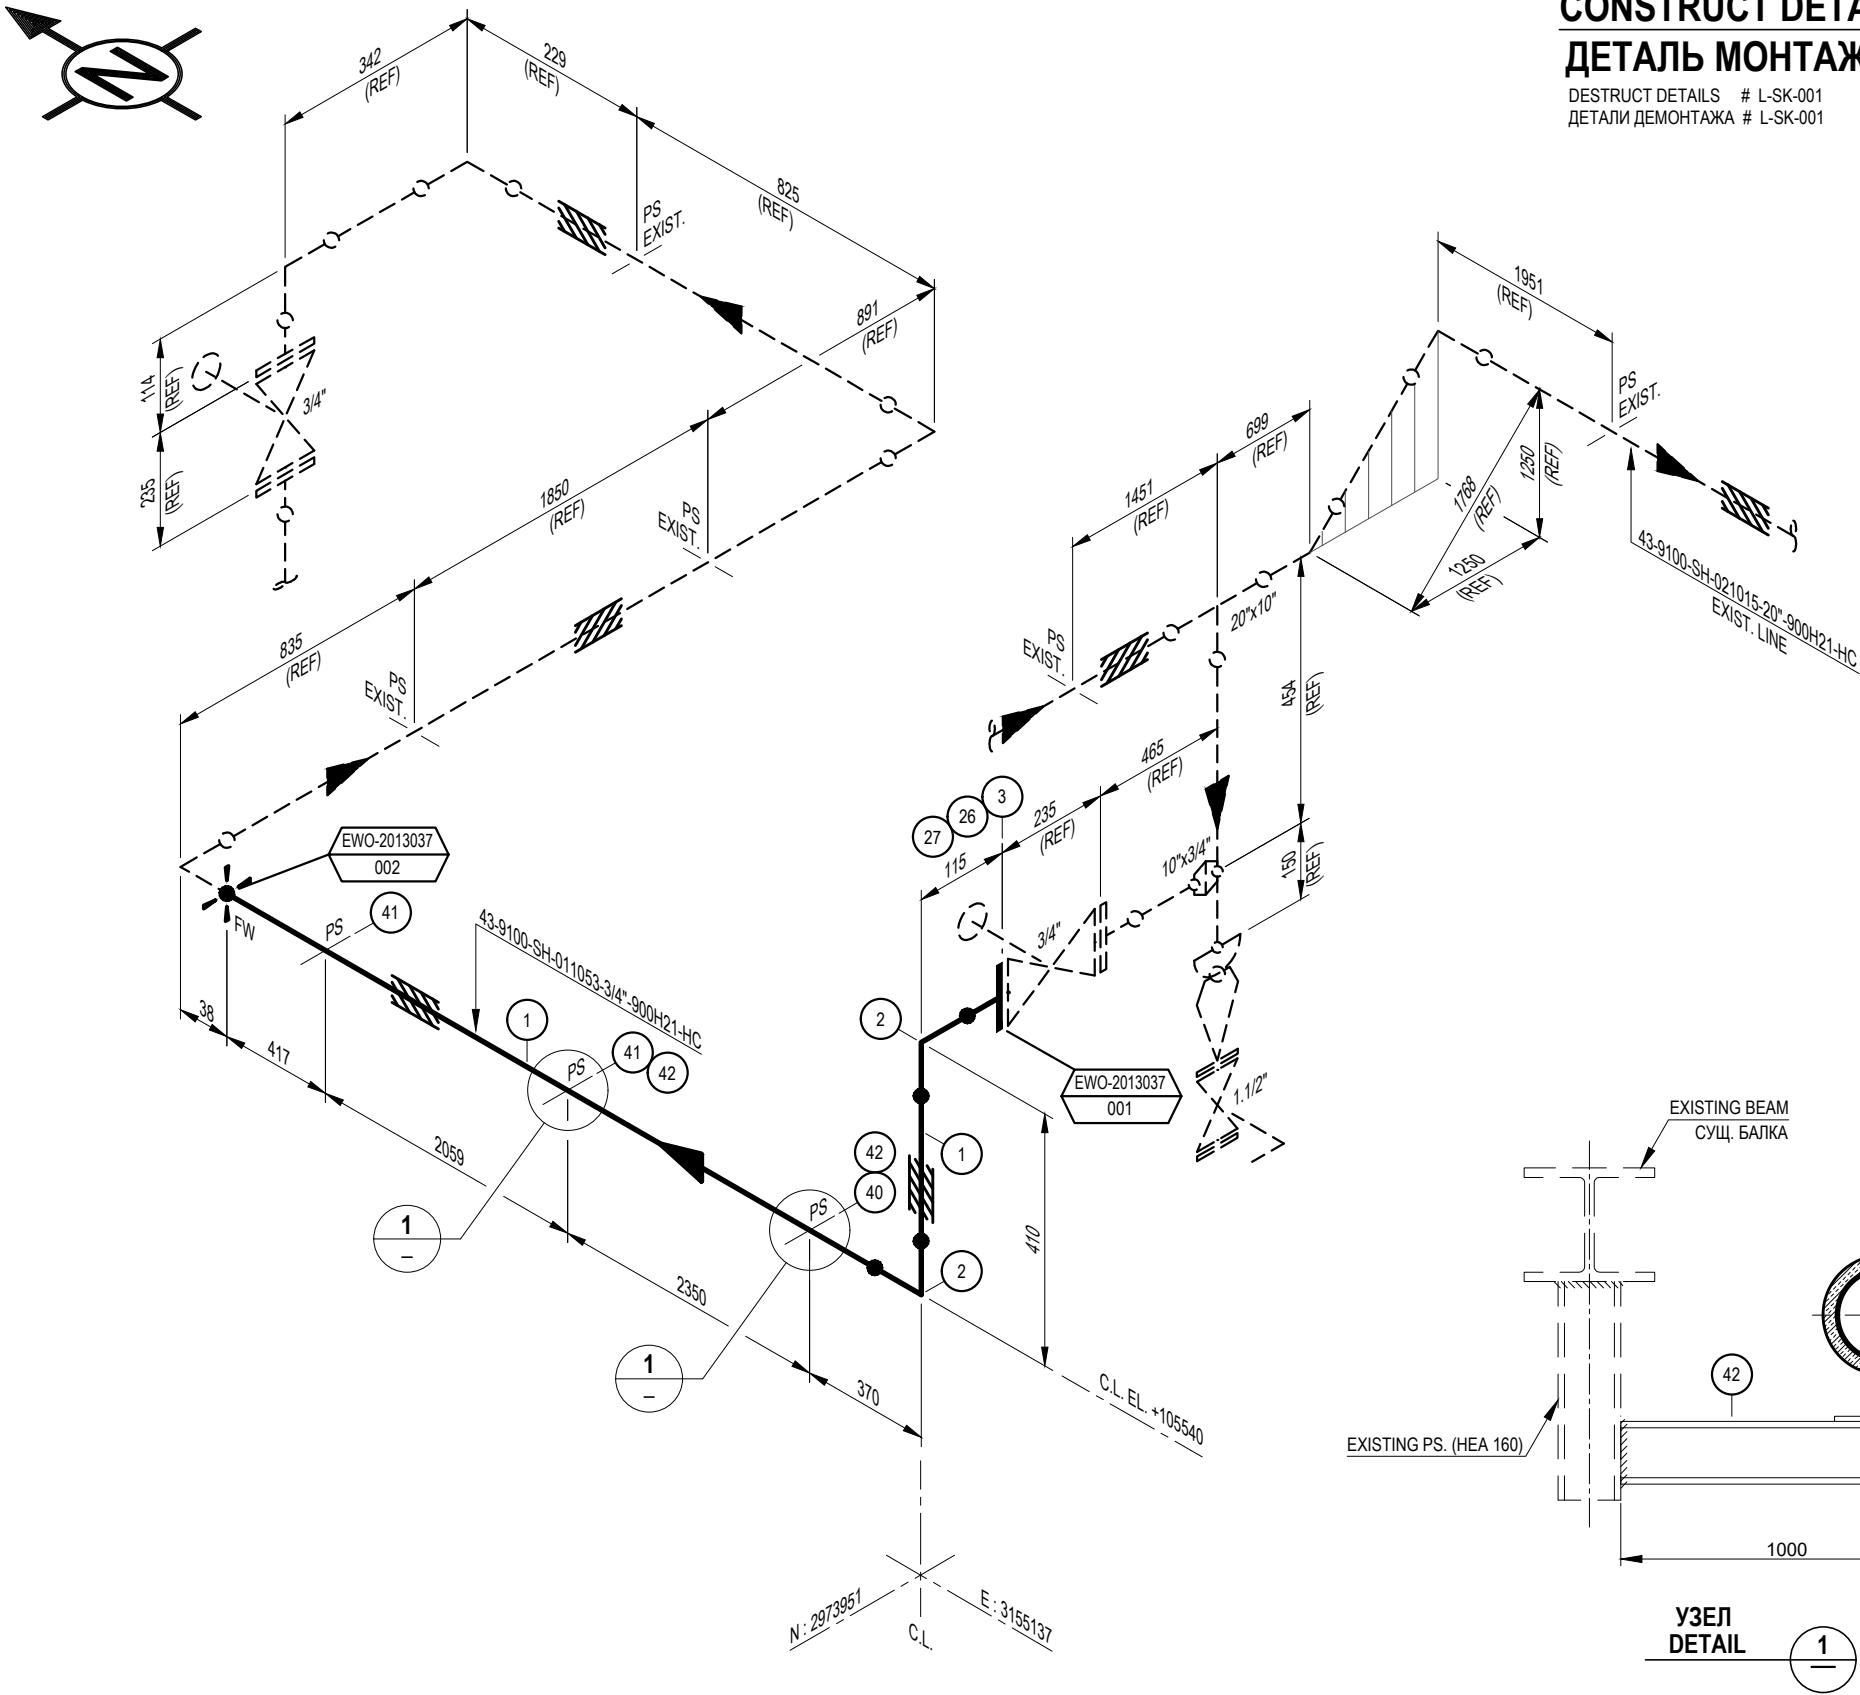

CONSTRUCT DETAIL
ДЕТАЛЬ МОНТАЖА

DESTRUCT DETAILS # L-SK-001
ДЕТАЛИ ДЕМОНТАЖА # L-SK-001

ITEM	QTY	NOM. DIA.	DESCRIPTION
SHOP MATERIAL			
1	5.6M	3/4"	PIPE SCH XS SMLS LTCS A333 GR.6.PE
2	2	3/4"	ELL BW 90 DEG LR SCH XS LTCS A420 WPL6
3	1	3/4"	FLG WN 1500# RF LTCS A350 LF2 CL.1 SCH XS
4			
5			
FIELD MATERIAL			
26	1	3/4"	GASKET 1500# 316SS SPIRAL WOUND GRAPHITE IR
27	4	M20	x 120 STUD-BOLT A320 GR L7M/A194 GR 7M (S3) WITH 2 NUTS
28			
29			
30			
31			
32			
33			
34			
35			
36			
37			
38			
39			
PIPE SUPPORT			
40	1	-	PIPE SUPPORT BY TCO STANDARD : NSPS-0253-A-3/4"
41	2	-	PIPE SUPPORT BY TCO STANDARD : NSPS-0149-A-3/4"
42	2	-	PIPE SUPPORT BY TCO STANDARD : P21-C4
43			
44			
K01	24/05/25	TCO REVIEW	HRKB EKUL EKUL
REV	DATE	REVISION	BY CH'K ENG



ТЕНІЗШЕВРОЙЛ
TENGIZCHEVROIL

TITLE

REINSTATE SUPPORT FOR ST-0095
PIPING ISOMETRIC
43-9100-SH-011053-3/4"-900H21-HC
ВОССТАНОВИТЬ ОПОРУ ДЛЯ КО-0095
ИЗОМЕТРИЯ ТРУБОПРОВОДА
43-9100-SH-011053-3/4"-900H21-HC

4. FOR SUPPORTS USE COATING SYSTEM 3.2.
ДЛЯ ОПОР ИСПОЛЬЗОВАТЬ СИСТЕМУ ПОКРЫТИЯ 3.2

NOTES / ПРИМЕЧАНИЯ

- PID DRG No 043-9100-BBB-PID-000-000-00009-01
СХЕМА ТРУБОПРОВОДОВ И КИП
- ALL ACTUAL DIMENSIONS SHALL BE FIELD VERIFIED BY CONTRACTOR PRIOR TO FABRICATION.
ВСЕ ФАКТИЧЕСКИЕ РАЗМЕРЫ ДОЛЖНЫ БЫТЬ ПРОВЕРЕНЫ ПОДРЯДЧИКОМ НА МЕСТЕ ДО ИЗГОТОВЛЕНИЯ.
- TCO WPS INDICATED FOR REFERENCE ONLY. CONTRACTOR SHOULD USE OWN TCO APPROVED WPS.
СВАРОЧНАЯ ПРОЦЕДУРА ТШО УКАЗАНА ТОЛЬКО ДЛЯ ССЫЛКИ.
ПОДРЯДЧИК ДОЛЖЕН ИСПОЛЬЗОВАТЬ СВОЮ СВАРОЧНУЮ ПРОЦЕДУРУ, УТВЕРЖДЕННУЮ ТШО.

LINE SPEC. СПЕЦИФИКАЦИЯ ЛИНИИ 900H21	INSULATION / ИЗОЛЯЦИЯ HC - 50mm	HYDROTEST ГИДРОИСПЫТАНИЕ 191 barg	PAINTING / COATING ПОКРАСКА / ПОКРЫТИЕ NOTE 4 12.7
DESIGN PRESSURE РАСЧЕТНОЕ ДАВЛЕНИЕ 82 barg	OPERATING PRESSURE РАБОЧЕЕ ДАВЛЕНИЕ 70 barg	NDT/ НЕРАЗРУШ. ИСП. VT-100% RT/UT-100%, MT/PT-100%	HARDNESS TEST ИСПЫТАНИЕ НА ТВЕРДОСТЬ N/A
DESIGN TEMPERATURE РАСЧЕТНАЯ ТЕМПЕРАТУРА -40°C / 410°C	OPERATING TEMPERATURE РАБОЧЕЕ ТЕМПЕРАТУРА 370°C / 380°C	STRESS RELIEF СНЯТИЕ НАПРЯЖЕНИЙ N/A	WPS# / СВАРОЧНАЯ ПРОЦЕДУРА 20AW NOTE 3

PROJ No.	EWO-2013037	
DRAWING No.	L-SK-002	
SCALE:	NTS	DATE: 24/05/25
REV	K01	