


4. APPLY CUT-LINE TAPE AS PER SP-26.
УСТАНОВИТЬ СПЕЦИАЛЬНУЮ ЛЕНТУ, ОПРЕДЕЛЯЮЩЕЙ
МЕСТО РЕЗКИ ТРУБОПРОВОДА, СОГЛАСНО ПТБ-26.

3. NDE TIE-IN POINT 002 TO DETERMINE ADEQUATE WALL THICKNESS FOR WELDING.
NDE REPORTS SHALL BE APPROVED BY TCO FER UNIT INSPECTOR PRIOR TO CUT.
ПРОВЕСТИ НМК ТОЧКИ ВРЕЗКИ 002 ПЕРЕД НАЧАЛОМ МЕХАНИЧЕСКИХ РАБОТ ДЛЯ ОПРЕДЕЛЕНИЯ ДОСТАТОЧНОЙ ТОЛЩИНЫ СТЕНКИ.
ОТЧЕТ ДОЛЖЕН БЫТЬ УТВЕРЖДЕН ИНСПЕКТОРОМ СТАЦИОНАРНОГО ОБОРУДОВАНИЯ ГРУППЫ НАДЕЖНОСТИ ПЕРЕД РЕЗКОЙ.

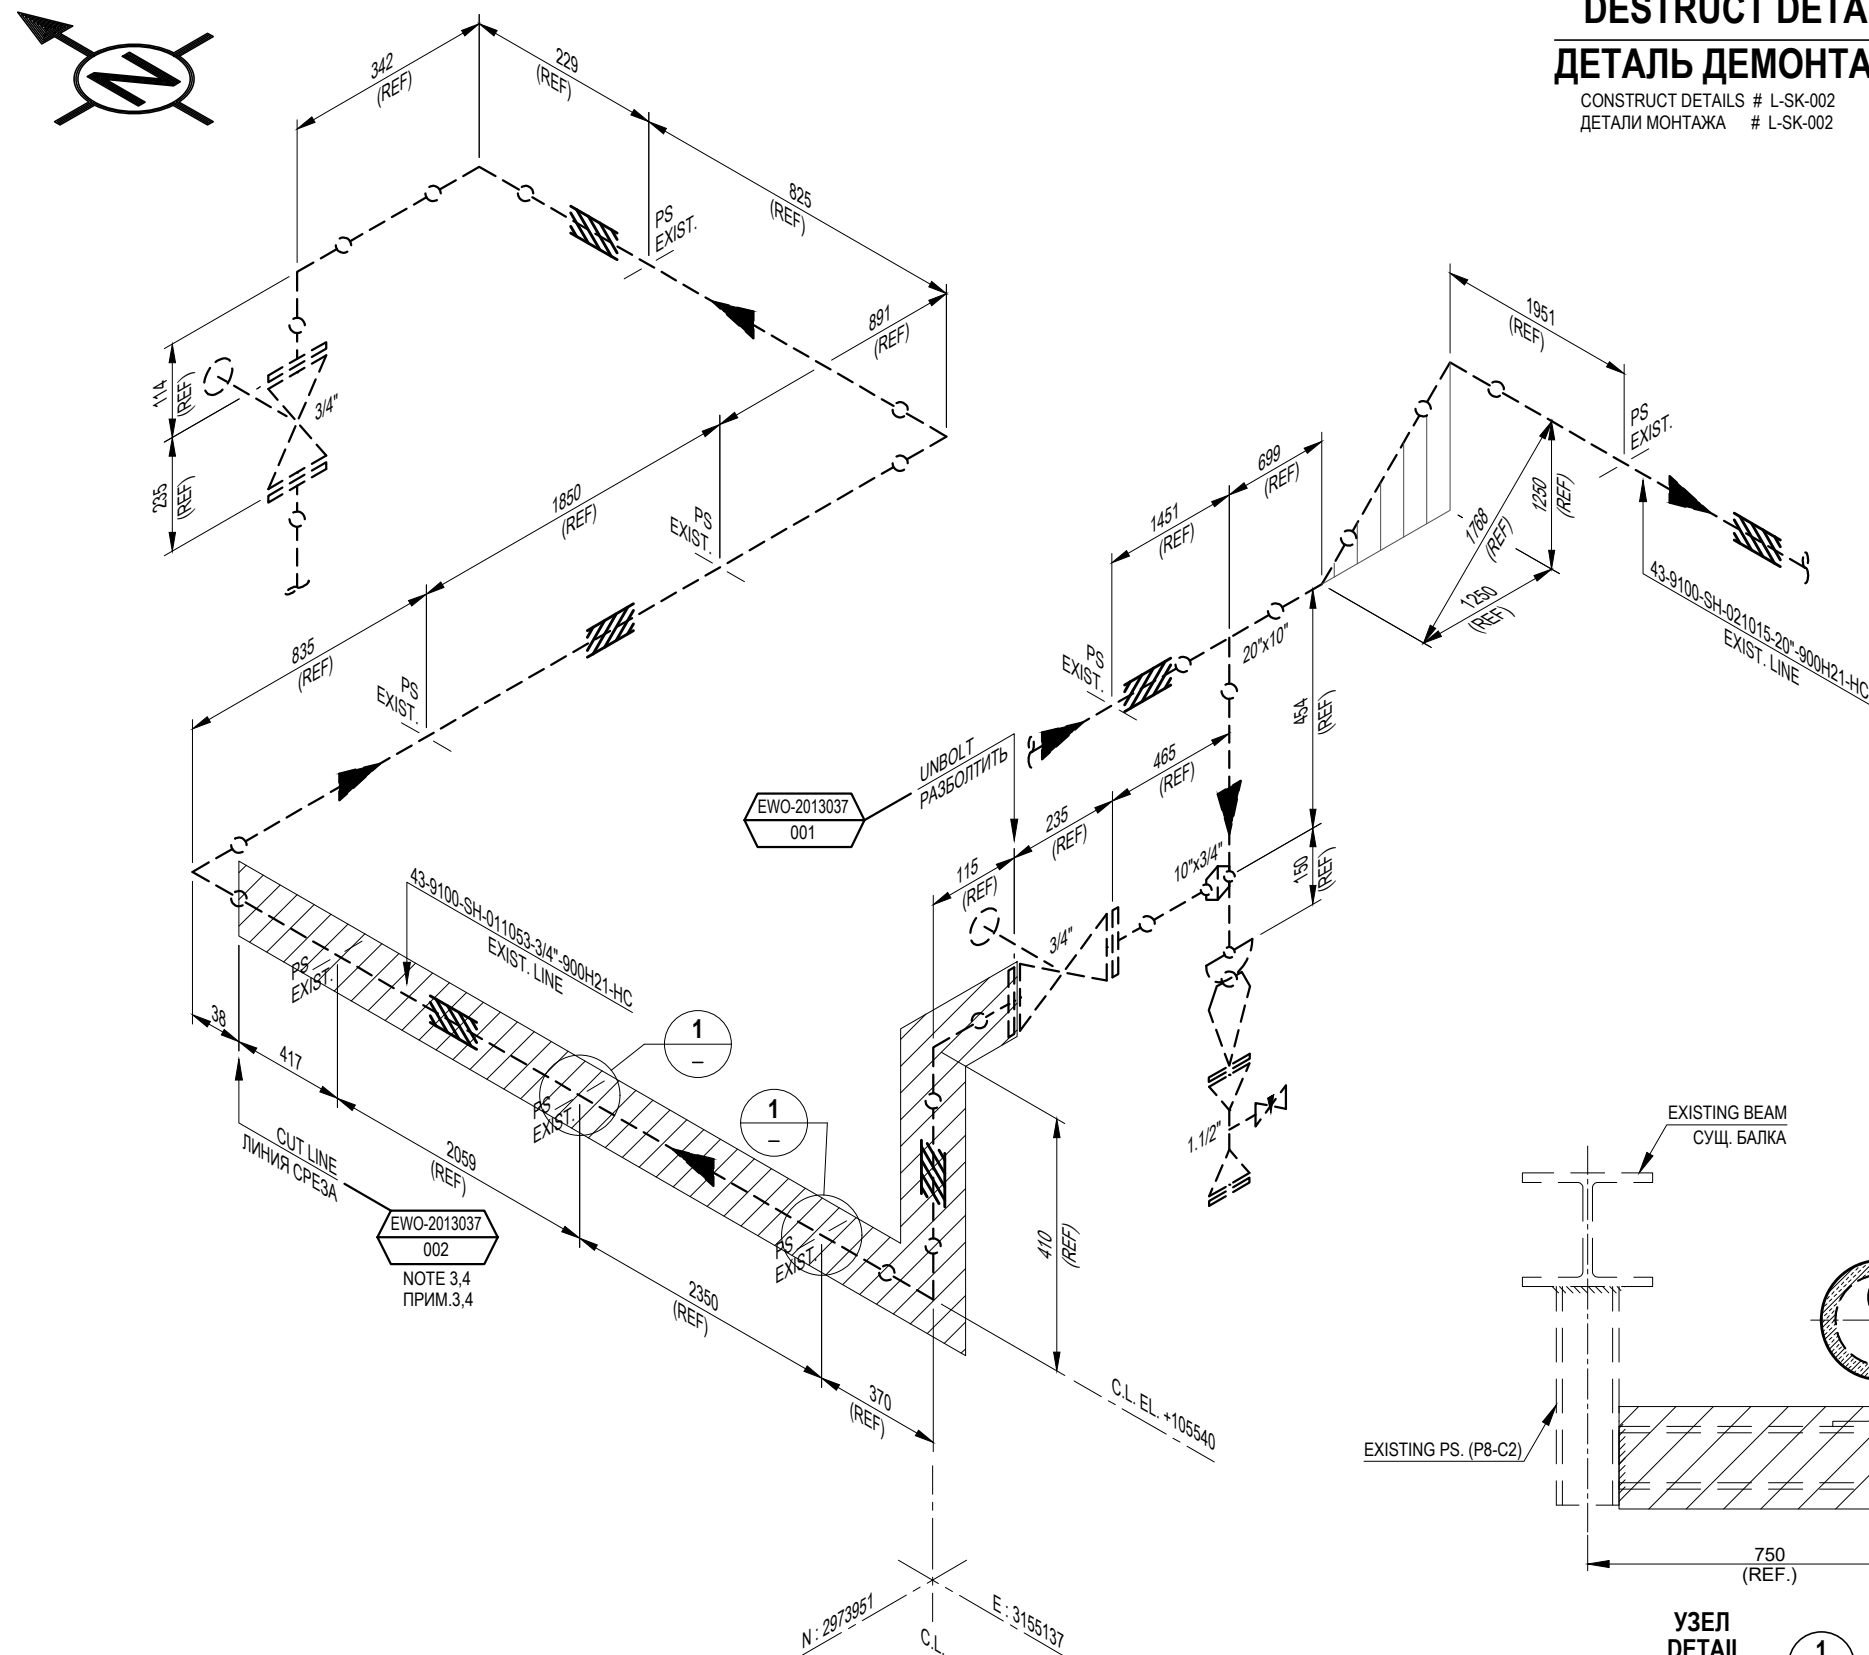

CONSTRUCT DETAILS # L-SK-002
ДЕТАЛИ МОНТАЖА # L-SK-002

K01	24/05/25	TCO REVIEW	HRKB	EKUL	EKUL
REV	DATE	REVISION	BY	CH'K	ENG



ТЕНІЗШЕВРОЙЛ
TENGIZCHEVROIL

TITLE

**REINSTATE SUPPORT FOR ST-0095
PIPING ISOMETRIC
43-9100-SH-011053-3/4"-900H21-HC
ВОССТАНОВИТЬ ОПОРУ ДЛЯ КО-0095
ИЗОМЕТРИЯ ТРУБОПРОВОДА
43-9100-SH-011053-3/4"-900H21-HC**

NOTES / ПРИМЕЧАНИЯ 1. PID DRG No 043-9100-BBB-PID-000-000-00009-01 СХЕМА ТРУБОПРОВОДОВ И КИП 2. ALL ACTUAL DIMENSIONS SHALL BE FIELD VERIFIED BY CONTRACTOR PRIOR TO FABRICATION. ВСЕ ФАКТИЧЕСКИЕ РАЗМЕРЫ ДОЛЖНЫ БЫТЬ ПРОВЕРЕНЫ ПОДРЯДЧИКОМ НА МЕСТЕ ДО ИЗГОТОВЛЕНИЯ.	LINE SPEC. СПЕЦИФИКАЦИЯ ЛИНИИ 900H21	INSULATION / ИЗОЛЯЦИЯ N/A	HYDROTEST ГИДРОИСПЫТАНИЕ N/A	PAINTING / COATING ПОКРАСКА / ПОКРЫТИЕ N/A	PROJ No. EWO-2013037	
	DESIGN PRESSURE РАСЧЕТНОЕ ДАВЛЕНИЕ N/A	OPERATING PRESSURE РАБОЧЕЕ ДАВЛЕНИЕ N/A	NDT/ НЕРАЗРУШ. ИСП. N/A	HARDNESS TEST ИСПЫТАНИЕ НА ТВЕРДОСТЬ N/A	DRAWING No. L-SK-001	REV K01
	DESIGN TEMPERATURE РАСЧЕТНАЯ ТЕМПЕРАТУРА N/A	OPERATING TEMPERATURE РАБОЧЕЕ ТЕМПЕРАТУРА N/A	STRESS RELIEF СНЯТИЕ НАПРЯЖЕНИЙ N/A	WPS# / СВАРОЧНАЯ ПРОЦЕДУРА N/A	SCALE: NTS	DATE: 24/05/25