


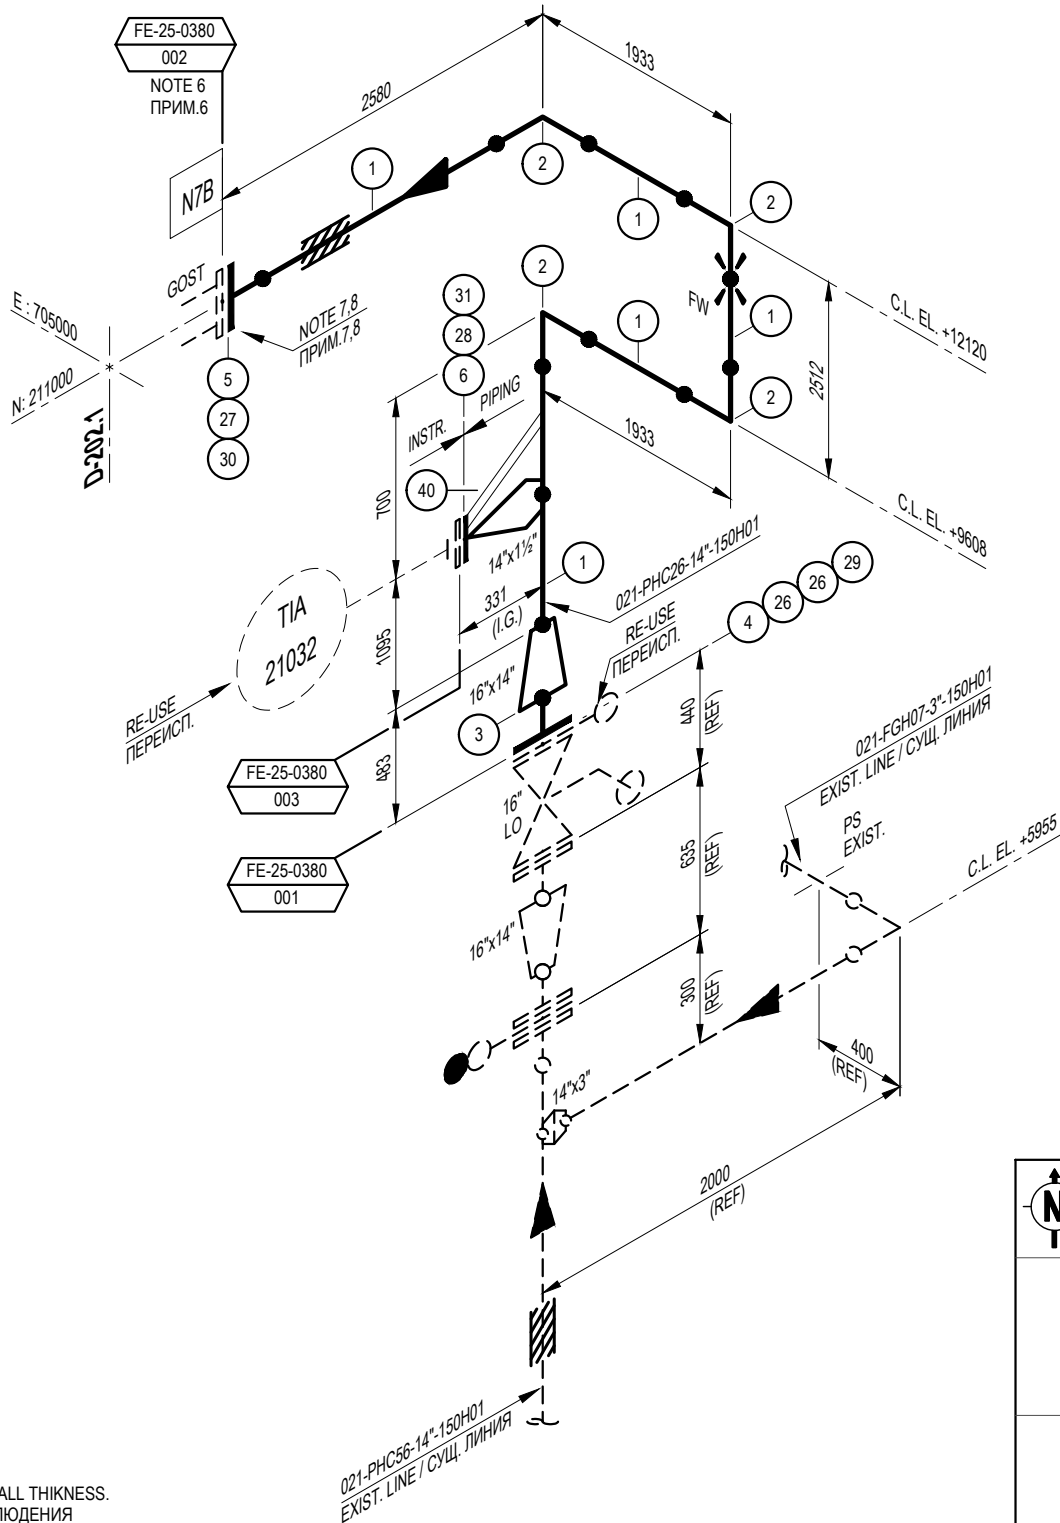

8. TAPER THE PIPE END INTERNALLY WITH A SLOPE 1:4 TO MEET FLANGE WALL THICKNESS. ВЫПОЛНИТЬ ФАСКУ ВНУТРИ ТРУБОПРОВОДА С УКЛОНОМ 1:4, ДЛЯ СОБЛЮДЕНИЯ ТОЛЩИНЕ СТЕНКИ ФЛАНЦА.
7. ENSURE FLANGE PROPERLY ORIENTED AND ALLIGNED WITH N7B NOZLE PRIOR FINAL WELDING PIPE WITH FLANGE. ПЕРЕД ПРИВАРКОЙ ТРУБЫ УБЕДИТЬСЯ, ЧТО ФЛАНЕЦ ОТЦЕНТРОВАН ПОЛОЖЕНИЮ НОЗЛА N7B.
6. CONTRACTOR TO DEMONSTRATE STRESS-FREE CONNECTION PRIOR TO HYDROTEST. ДО НАЧАЛА ГИДРОИСПЫТАНИЯ ПОДРЯДЧИКУ СЛЕДУЕТ ПРОДЕМОНСТРИРОВАТЬ, ЧТО СОЕДИНЕНИЕ НЕ ПОДВЕРГАЕТСЯ НАГРУЗКАМ.
5. CONTRACTOR TO DETERMINATE AND ALLOCATE FIELD WELDS AS REQUIRED. ПОДРЯДЧИК ОПРЕДЕЛЯЕТ И РАСПРЕДЕЛЯЕТ МОНТАЖНЫЕ ШВЫ ПО МЕРЕ НЕОБХОДИМОСТИ.
4. TCO WPS INDICATED FOR REFERENCE ONLY. CONTRACTOR SHOULD USE OWN TCO APPROVED WPS. СВАРОЧНАЯ ПРОЦЕДУРА ТШО УКАЗАНА ТОЛЬКО ДЛЯ ССЫЛКИ. ПОДРЯДЧИК ДОЛЖЕН ИСПОЛЬЗОВАТЬ СВОЮ СВАРОЧНУЮ ПРОЦЕДУРУ, УТВЕРЖДЕННУЮ ТШО.

- NOTES / ПРИМЕЧАНИЯ
1. PID DRG No 1-200_1-B-5006-250380, 1-200_1-004-250380
СХЕМА ТРУБОПРОВОДОВ И КИП
2. ALL DIMENSIONS SHALL BE FIELD VERIFIED BY CONTRACTOR PRIOR TO FABRICATION.
ВСЕ РАЗМЕРЫ ДОЛЖНЫ БЫТЬ ПРОВЕРЕНЫ ПОДРЯДЧИКОМ НА МЕСТЕ ДО ИЗГОТОВЛЕНИЯ.
3. TES L-ST-2056 LINE CLASS 150H21 MATERIAL USED LIEU TO LEGACY LINE CLASS 150H01 MATERIAL.
МАТЕРИАЛ TES L-ST-2056 КЛАСС ЛИНИИ 150H21 ИСПОЛЬЗОВАН ВМЕСТО МАТЕРИАЛА КЛАССА ЛИНИИ 150H01.


LINE SPEC. СПЕЦИФИКАЦИЯ ЛИНИИ	NOTE 3 150H01	INSULATION / ИЗОЛЯЦИЯ HC 80mm	HYDROTEST ГИДРОИСПЫТАНИЕ 14.5 barg	PAINTING / COATING ПОКРАСКА / ПОКРЫТИЕ 12.1
DESIGN PRESSURE РАСЧЕТНОЕ ДАВЛЕНИЕ 9.6 barg	OPERATING PRESSURE РАБОЧЕЕ ДАВЛЕНИЕ 8 barg	NDT/ НЕРАЗРУШ. ИСП. VT-100% MT/PT-100%, RT-5%	HARDNESS TEST ИСПЫТАНИЕ НА ТВЕРДОСТЬ N/A	
DESIGN TEMPERATURE РАСЧЕТНАЯ ТЕМПЕРАТУРА 200°C	OPERATING TEMPERATURE РАБОЧЕЕ ТЕМПЕРАТУРА 172°C	STRESS RELIEF СНЯТИЕ НАПРЯЖЕНИЙ N/A	WPS# / СВАРОЧНАЯ ПРОЦЕДУРА ≤3"-20AW, >3"-21AW NOTE 4	

CONSTRUCT DETAIL
ДЕТАЛЬ МОНТАЖА

DESTRUCT DETAILS # 011-0200-LLL-ISO-20261-01
ДЕТАЛИ ДЕМОНТАЖА # 011-0200-LLL-ISO-20261-01

WO # 2200623

MOC # 1033298

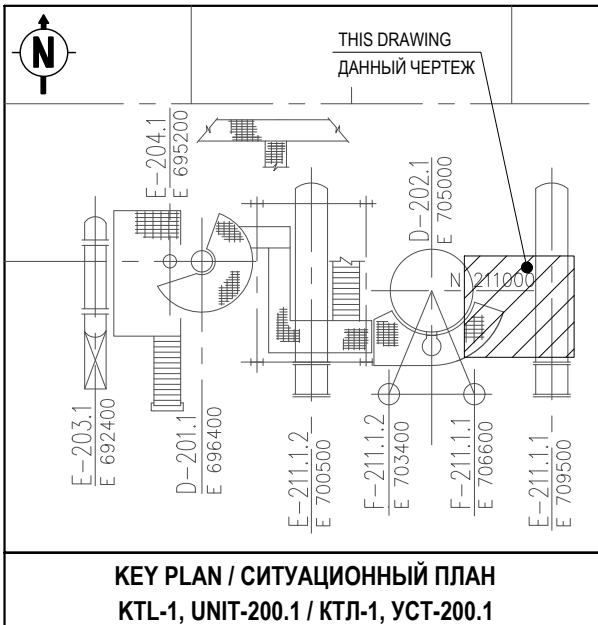

ITEM	QTY	NOM. DIA.	DESCRIPTION
SHOP MATERIAL			
1	11M	14"	PIPE SCH STD SMLS LTCS A333 GR.6 BE
2	4	14"	ELL BW 90 DEG LR SCH STD LTCS A420 WPL6
3	1	16"	x 14" REDUCER CONC SCH 20/STD LTCS A420 WPL6
4	1	16"	FLG WN 150# RF LTCS A350 LF2 CL.1 SCH 20
5	1	14"	FLG CS DN 350 PN1.6 RF GOST 12821-80 (OUT OF SPEC.)
6	1	14"	x 1 1/2" NIPOFLANGE 300# RF SCH STD/160 LTCS A350 LF2 CL.1
7			
8			
FIELD MATERIAL			
26	2	16"	GASKET 150# 316SS SPIRAL WOUND GRAPHITE IR
27	1	14"	GASKET DN 350 PN1.6 RF GOST (OUT OF SPEC.)
28	1	1 1/2"	GASKET 300# 316SS SPIRAL WOUND GRAPHITE IR
29	16	M27	x 170 STUD-BOLT A320 GR L7M/A194 GR 7M (S3) WITH 2 NUTS
30	16	M24	x 130 STUD-BOLT A320 GR L7M/A194 GR 7M (S3) WITH 2 NUTS
31	4	M20	x 100 STUD-BOLT A320 GR L7M/A194 GR 7M (S3) WITH 2 NUTS
32			
33			
34			
35			
36			
37			
38			
39			
PIPE SUPPORT			
40	1	-	PIPE SUPPORT BY TCO STANDARD : GSW1
41			
42			
43			
44			

U01	29/01/26	CONSTRUCTION OR USE	AIXN	YNYE	BXEX
REV	DATE	REVISION	BY	CHK	ENG

ТЕНІЗШЕВРОЙЛ

TENGIZCHEVROIL

TITLE

THE LOOP EXPANSION INSTALLATION PIPING ISOMETRIC 021-PHC26-14"-150H01

УСТАНОВКА ТРУБНОГО КОМПЕНСАТОРА ИЗОМЕТРИЯ ТРУБОПРОВОДА 021-PHC26-14"-150H01

PROJ No.	FE-25-0380	REV	U01
DRAWING No.	011-0200-LLL-ISO-20262-01		
SCALE:	NTS	DATE:	12/01/26