


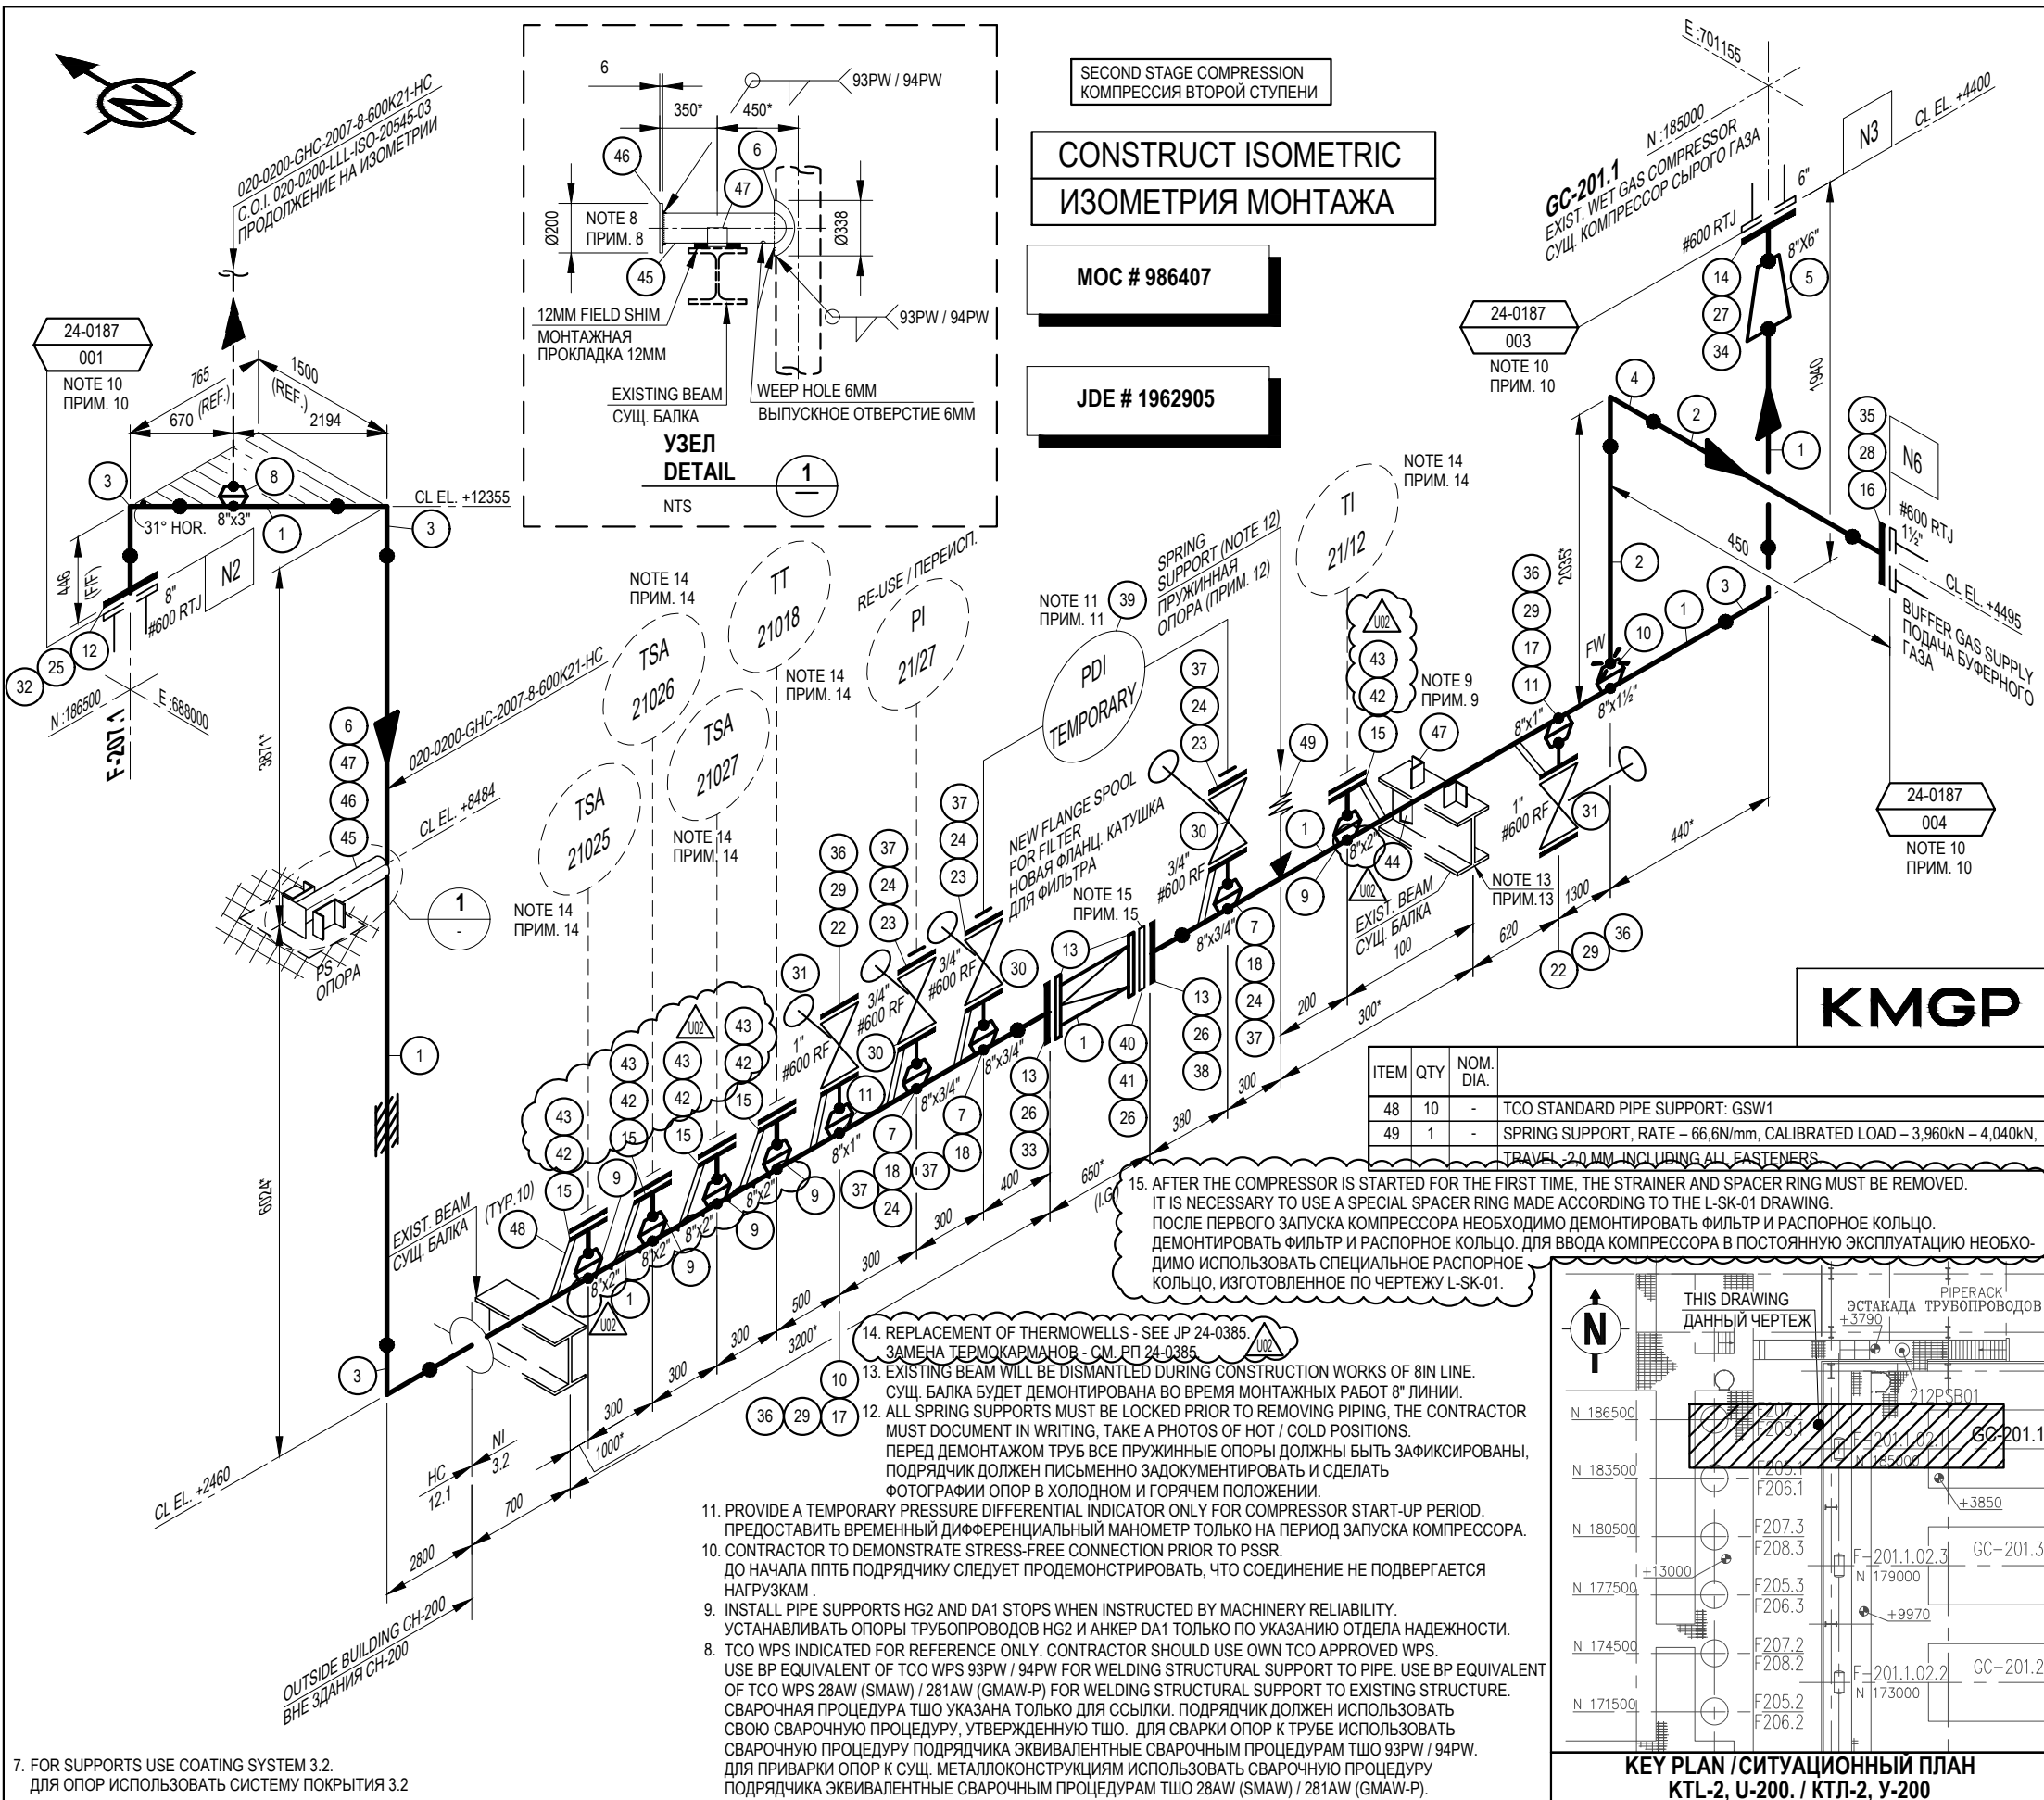

NOTES / ПРИМЕЧАНИЯ		LINE SPEC. СПЕЦИФИКАЦИЯ ЛИНИИ	INSULATION / ИЗОЛЯЦИЯ	HYDROTEST ГИДРОИСПЫТАНИЕ	PAINTING / COATING ПОКРАСКА / ПОКРЫТИЕ
1. PID DRG No 2-200-B-5010-240187, 2-200-009-240187. СХЕМА ТРУБОПРОВОДОВ И КИП 2-200-B-5010-240187, 2-200-009-240187.		600K21	3" - 40MM HC 8" - 50MM HC	120barg	NOTE 7 / ПРИМ. 7 3.2, 12.1
2. DESTRUCT DETAIL SEE DRAWING 020-0200-LLL-ISO-20545-01. ДЕТАЛИ ДЕМОНТАЖА СМ. ЧЕРТЕЖ 020-0200-LLL-ISO-20545-01.		DESIGN PRESSURE РАСЧЕТНОЕ ДАВЛЕНИЕ	OPERATING PRESSURE РАБОЧЕЕ ДАВЛЕНИЕ	NDT / НЕРАЗРУШ. ИСП.	HARDNESS TEST ИСПЫТАНИЕ НА ТВЕРДОСТЬ
3. CONTRACTOR TO VERIFY ALL DIMENSIONS AND TIE-IN LOCATIONS PRIOR TO FABRICATION. ПЕРЕД ИЗГОТОВЛЕНИЕМ ПОДРЯДЧИК ПРОВЕРЯЕТ ВСЕ РАЗМЕРЫ И РАСПОЛОЖЕНИЕ ТОЧЕК ВРЕЗОК.		80barg	22.5barg	VT-100%, RT/UT-100%, MT-100%	200 HB
4. PWHT TEMPERATURE SHALL COMPLY WITH 23-0007-MI. ТЕМПЕРАТУРА ПСТО ДОЛЖНА СООТВЕТСТВОВАТЬ 23-0007-MI.		DESIGN TEMPERATURE РАСЧЕТНАЯ ТЕМПЕРАТУРА	OPERATING TEMPERATURE РАБОЧАЯ ТЕМПЕРАТУРА	STRESS RELIEF СНЯТИЕ НАПРЯЖЕНИЙ	NOTE 4 ПРИМ. 4 YES
5. FW - INDICATES FIELD WELD. FW - ПОКАЗЫВАЕТ МЕСТО МОНТАЖНОГО ШВА.					
6. CONTRACTOR TO DETERMINATE AND ALLOCATE FIELD WELDS AS REQUIRED. ПОДРЯДЧИК ОПРЕДЕЛЯЕТ И РАСПРЕДЕЛЯЕТ МОНТАЖНЫЕ ШВЫ ПО МЕРЕ НЕОБХОДИМОСТИ.		80°C	47°C		

ITEM	QTY	NOM. DIA.	DESCRIPTION
SHOP MATERIAL			
1	25M	8"	PIPE SCH XS SMLS LTCS A333 GR.6 BE
2	2.5M	1½"	PIPE SCH 160 SMLS LTCS A333 GR.6 PE
3	4	8"	ELL BW 90 DEG LR SCH XS LTCS A420 WPL6
4	1	1½"	ELL BW 90 DEG LR SCH 160 LTCS A420 WPL6
5	1	8"x6"	REDUCER CONC SCH XS LTCS A420 WPL6
6	0.5M	8"	REINFORCING PAD FROM PIPE SCH XS SMLS LTCS A333 GR.6 BE
7	3	8"x3/4"	WELDOLET SCH XS/160 LTCS A350 LF2 CL.1
8	1	8"x3"	WELDOLET SCH XS LTCS A350 LF2 CL.1
9	5	8"x2"	WELDOLET SCH SCH 80 (XS) LTCS A350 LF2 CL.1 (OUT OF SPEC)
10	1	8 x1½"	WELDOLET SCH XS/160 LTCS A350 LF2 CL.1
11	2	8"x1"	WELDOLET SCH XS/160 LTCS A350 LF2 CL.1
12	1	8"	FLG WN 600# RTJ LTCS A350 LF2 CL.1 SCH XS (OUT OF SPEC)
13	4	8"	FLG WN 600# RF LTCS A350 LF2 SCH XS
14	1	6"	FLG WN 600# RTJ LTCS A350 LF2 CL.1 SCH XS (OUT OF SPEC)
15	5	2"	FLG WN 600# RF LTCS A350 LF2 CL.1 SCH SCH 80 (XS) (OUT OF SPEC)
16	1	1½"	FLG WN 600# RTJ LTCS A350 LF2 CL.1 SCH 160 (OUT OF SPEC)
17	2	1"	FLG WN 600# RF LTCS A350 LF2 CL.1 SCH 160
18	3	3/4"	FLG WN 600# RF LTCS A350 LF2 CL.1 SCH 160
FIELD MATERIALS			
22	2	1"	FLG BLIND 600# RF LTCS A350 LF2 CL.1
23	3	3/4"	FLANGE ADAPTER 600# RF 316 SS x 12 MM TUBE
24	6	3/4"	GASKET 600# 316SS SP WND GRAPHITE IR
25	1	8"	GASKET 600# RTJ SS OCTAGONAL RING R49 (OUT OF SPEC)
26	3	8"	GASKET 600# 316SS SP WND GRAPHITE IR
27	1	6"	GASKET 600# RTJ SS OCTAGONAL RING R45 (OUT OF SPEC)
28	1	1½"	GASKET 600# RTJ SS OCTAGONAL RING R20 (OUT OF SPEC)
29	4	1"	GASKET 600# 316SS SP WND GRAPHITE IR
30	3	3/4"	GATE 600# RF LTCS A350 LF2 TRIM 16 WEDGE HW
31	2	1"	GATE 600# RF LTCS A350 LF2 TRIM 16 WEDGE HW
32	12	M30	x 200 STUD-BOLT A320 GR L7M/A194 GR 7M (S3) WITH 2 NUTS
33	12	M30	x 205 STUD-BOLT A320 GR L7M/A194 GR 7M (S3) WITH 2 NUTS
34	12	M27	x 185 STUD-BOLT A320 GR L7M/A194 GR 7M (S3) WITH 2 NUTS
35	4	M20	x 115 STUD-BOLT A320 GR L7M/A194 GR 7M (S3) WITH 2 NUTS
36	16	M16	x 100 STUD-BOLT A320 GR L7M/A194 GR 7M (S3) WITH 2 NUTS
37	24	M16	x 95 STUD-BOLT A320 GR L7M/A194 GR 7M (S3) WITH 2 NUTS
38	12	M30	x 245 STUD-BOLT A320 GR L7M/A194 GR 7M (S3) WITH 2 NUTS
39	1	-	TEMP PDI (PROVIDED BY INSTRUMENT)
40	1	8"	TEMP CONICAL TYPE STRAINER 600# RF SS 316L
41	1	8"	PADDLE SPACER 600# RF LTCS A516 GR70 (OUT OF SPEC)
42	40	M16	x 115 STUD-BOLT A320 GR L7M/A194 GR 7M (S3) WITH 2 NUTS
43	5	2"	GASKET 600# 316SS SPIRAL WOUND GRAPHITE IR
PIPE SUPPORT			
44	1	-	TCO STANDARD PIPE SUPPORT: DA1-8
45	1M	6"	PIPE SCH XS SMLS LTCS A333 GR.6 BE
46	1	-	TCO STANDARD PIPE SUPPORT: T1-6
47	2	-	TCO STANDARD PIPE SUPPORT: HG2-C
U02	16/01/25	CONSTRUCTION OR USE	PS SIZH SIZH
U01	26/12/24	CONSTRUCTION OR USE	TAI YF ALT
REV	DATE	REVISION	BY CHK ENG



ТЕНІЗШЕВРОЙЛ

TENGIZCHEVROIL

TITLE			
KTL-2 F-207.1 SWEET GAS LINE REPLACEMENT PIPING ISOMETRIC 020-0200-GHC-2007-8"-600K21-NI КТЛ-2 F-207.1 ЗАМЕНА ЛИНИИ КИСЛОГО ГАЗА ИЗОМЕТРИЯ ТРУБОПРОВОДА 020-0200-GHC-2007-8"-600K21-NI			
DRAWN BY TAI	CHECKED BY YF	PROJ No FE-24-0187	REV U02
ENGINEER ALT	SUPERVISOR AK	DRAWING No. 020-0200-LLL-ISO-20545-02	
OPERATIONS	PROJ MGR	SCALE: N.T.S	DATE: 25/06/24