


THIS DRAWING AND THE DESIGN IT COVERS ARE THE PROPERTY OF TENGIZCHEVROIL. THEY ARE MERELY LOANED AND ON THE BORROWERS EXPRESS AGREEMENT THAT THEY WILL NOT BE REPRODUCED COPIED LOANED EXHIBITED NOR USED EXCEPT IN THE LIMITED WAY AND PRIVATE USE PERMITTED AND WRITTEN CONSENT GIVEN BY TENGIZCHEVROIL TO THE BORROWER.

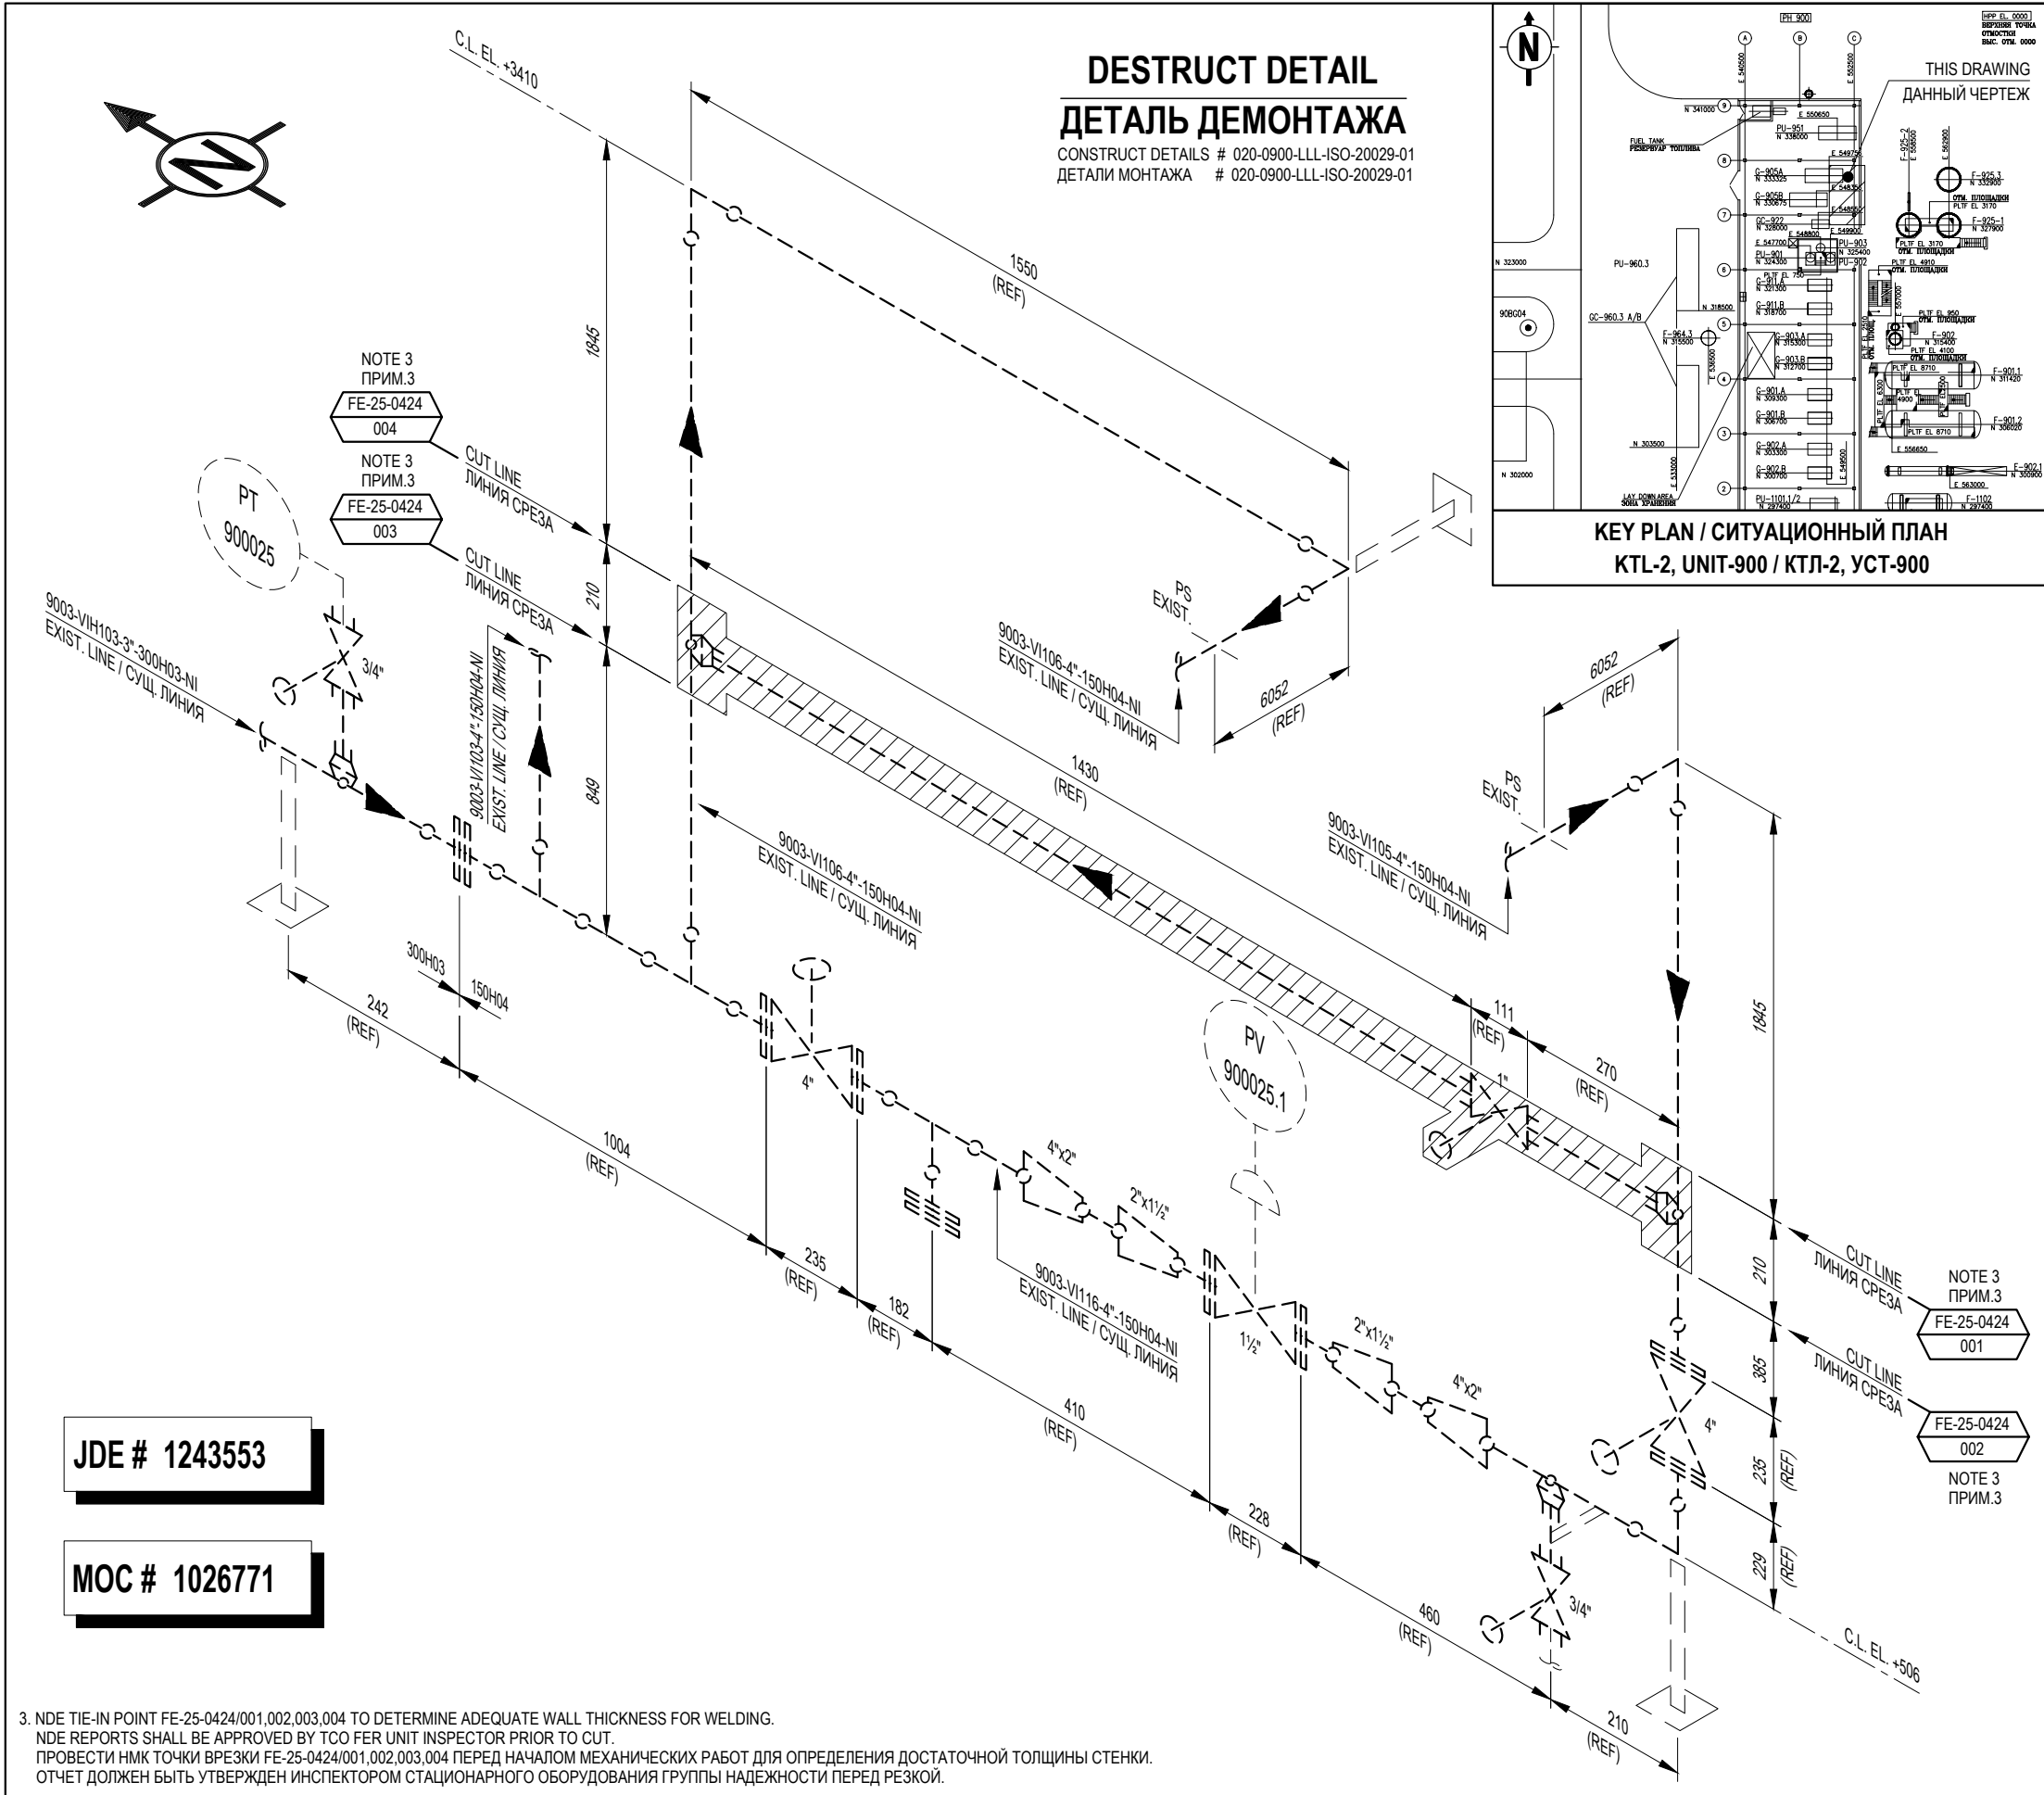


JDE # 1243553

МОС # 1026771

DESTRUCT DETAIL
ДЕТАЛЬ ДЕМОНТАЖА

CONSTRUCT DETAILS # 020-0900-LLL-ISO-20029-01
ДЕТАЛИ МОНТАЖА # 020-0900-LLL-ISO-20029-01

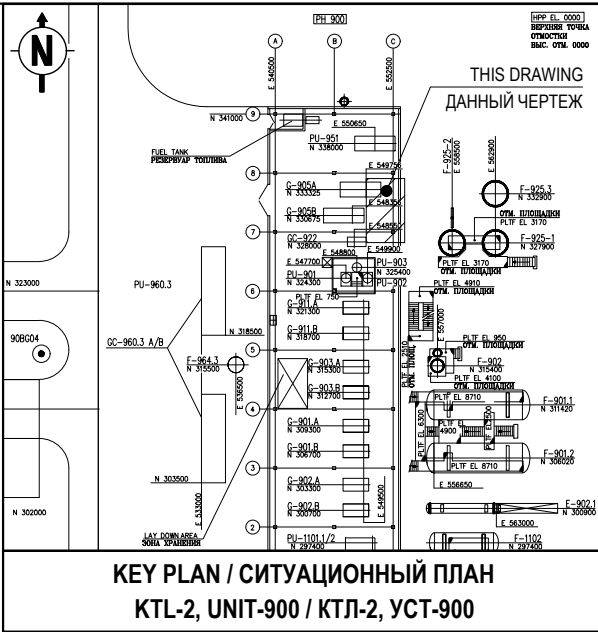

KEY PLAN / СИТУАЦИОННЫЙ ПЛАН
KTL-2, UNIT-900 / КТЛ-2, УСТ-900

ITEM	QTY	NOM. DIA.	DESCRIPTION
1			SHOP MATERIAL
2			
3			
25			FIELD MATERIAL
26			
27			
28			
29			
30			
31			
32			
33			
34			
35			
36			
37			
38			
39			PIPE SUPPORT
40			
41			
42			
43			
44			

U01	18/11/25	TCO REVIEW	ZBAS	ZBAS	XQTO
REV	DATE	REVISION	BY	CHK	ENG



ТЕНІЗШЕВРОЙЛ
TENGIZCHEVROIL

TITLE
REPLACE BYPASS VALVE 23-0900-PV-900025.1
PIPING ISOMETRIC
9003-VI106-4"-150H04-NI
ЗАМЕНА БАЙПАС КЛАПАН 23-0900-PV-900025.1
ИЗОМЕТРИЯ ТРУБОПРОВОДА
9003-VI106-4"-150H04-NI

3. NDE TIE-IN POINT FE-25-0424/001,002,003,004 TO DETERMINE ADEQUATE WALL THICKNESS FOR WELDING.
NDE REPORTS SHALL BE APPROVED BY TCO FER UNIT INSPECTOR PRIOR TO CUT.
ПРОВЕСТИ НМК ТОЧКИ ВРЕЗКИ FE-25-0424/001,002,003,004 ПЕРЕД НАЧАЛОМ МЕХАНИЧЕСКИХ РАБОТ ДЛЯ ОПРЕДЕЛЕНИЯ ДОСТАТОЧНОЙ ТОЛЩИНЫ СТЕНКИ.
ОТЧЕТ ДОЛЖЕН БЫТЬ УТВЕРЖДЕН ИНСПЕКТОРОМ СТАЦИОНАРНОГО ОБОРУДОВАНИЯ ГРУППЫ НАДЕЖНОСТИ ПЕРЕД РЕЗКОЙ.

NOTES / ПРИМЕЧАНИЯ	LINE SPEC. СПЕЦИФИКАЦИЯ ЛИНИИ	INSULATION / ИЗОЛЯЦИЯ	HYDROTEST ГИДРОИСПЫТАНИЕ	PAINTING / COATING ПОКРАСКА / ПОКРЫТИЕ	PROJ No.
1. PID DRG No 2-900_3-B-3220-250424D. СХЕМА ТРУБОПРОВОДОВ И КИП	150H04	N/A	N/A	N/A	FE-25-0424
2. ALL DIMENSIONS SHALL BE FIELD VERIFIED BY CONTRACTOR PRIOR TO DESTRUCT ACTIVITIES. ВСЕ РАЗМЕРЫ ДОЛЖНЫ БЫТЬ ПРОВЕРЕНЫ ПОДРЯДЧИКОМ НА МЕСТЕ ДО ДЕМОНТАЖА.	N/A	OPERATING PRESSURE РАБОЧЕЕ ДАВЛЕНИЕ	NDT/ НЕРАЗРУШ. ИСП.	HARDNESS TEST ИСПЫТАНИЕ НА ТВЕРДОСТЬ	DRAWING No.
	N/A	OPERATING TEMPERATURE РАБОЧАЯ ТЕМПЕРАТУРА	STRESS RELIEF СНЯТИЕ НАПРЯЖЕНИЙ	WPS# / СВАРОЧНАЯ ПРОЦЕДУРА	020-0900-LLL-ISO-20028-01
	N/A	N/A	N/A	N/A	SCALE: NTS
					DATE: 11/11/25
					REV U01