


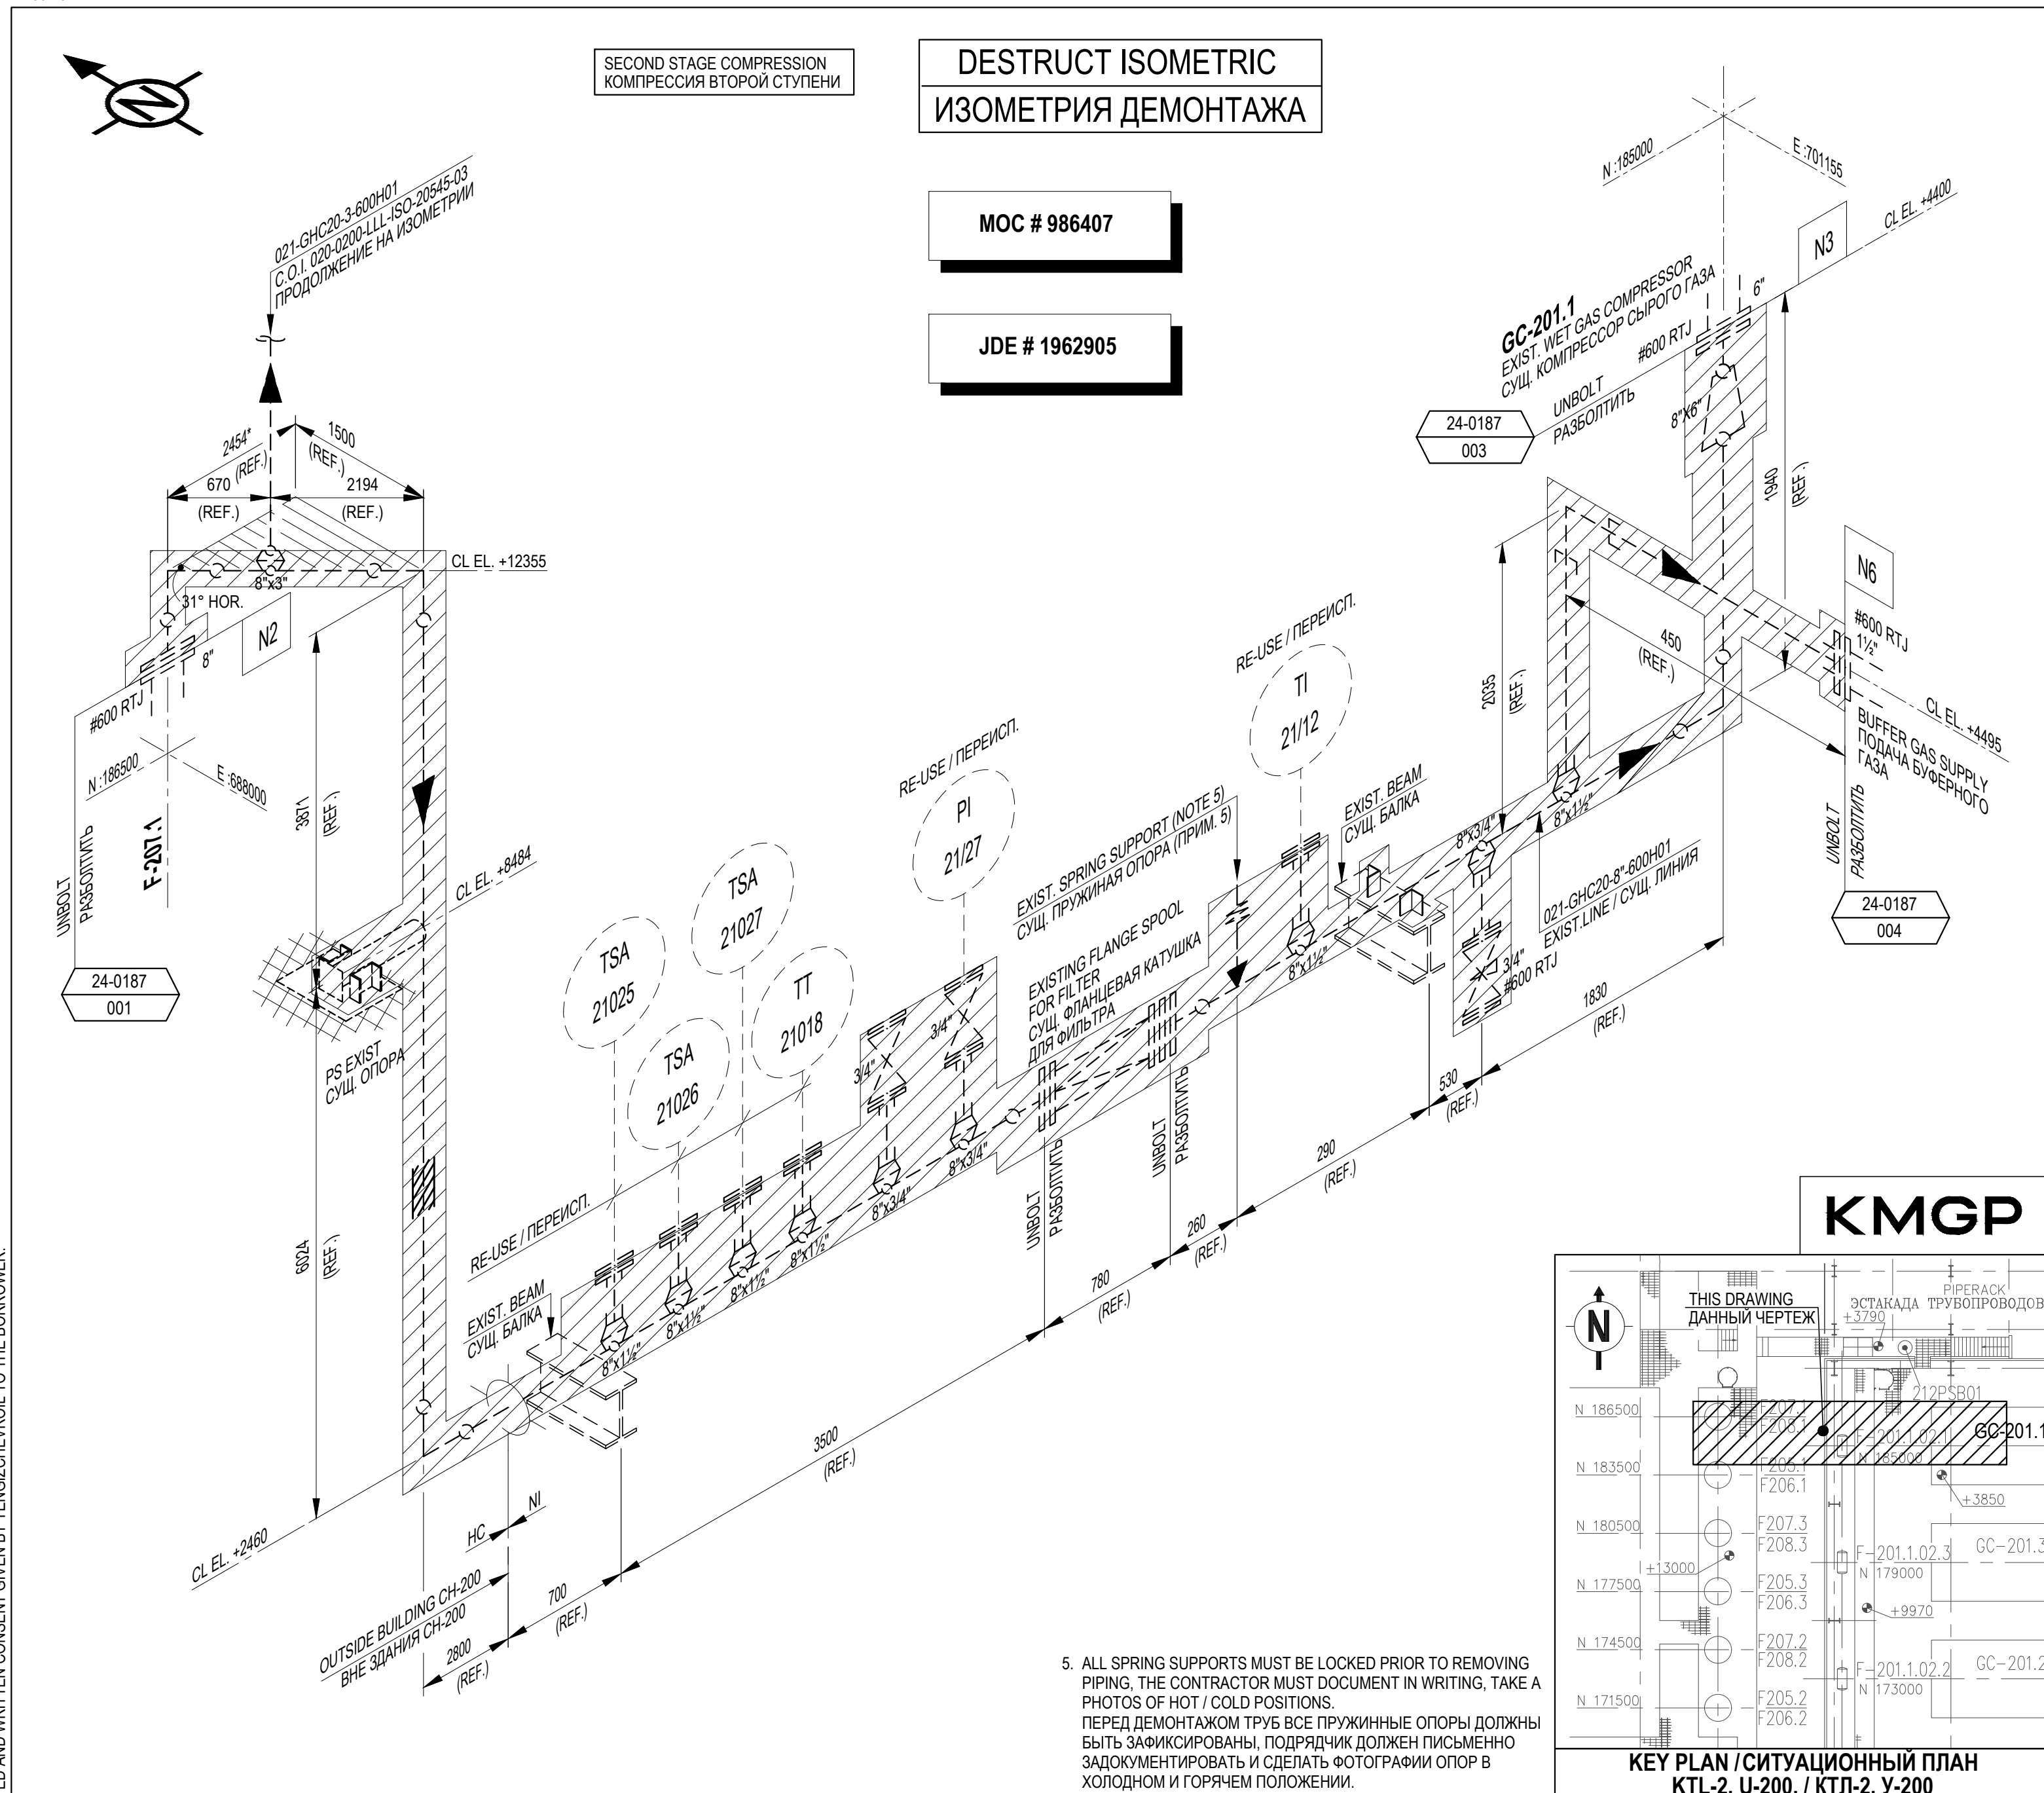

ITEM	QTY	NOM. DIA.	DESCRIPTION
			SHOP MATERIAL
1			
2			
U01	26/12/24	CONSTRUCTION OR USE	TAIYFALT
REV	DATE	REVISION	BYCHKENG
 ТЕНГІЗШЕВРОЙЛ TENGIZCHEVROIL			
TITLE			
KTL-2 F-207.1 SWEET GAS LINE REPLACEMENT PIPING ISOMETRIC 021-GHC20-8"-600H01			
КТЛ-2 F-207.1 ЗАМЕНА ЛИНИИ КИСЛОГО ГАЗА ИЗОМЕТРИЯ ТРУБОПРОВОДА 021-GHC20-8"-600H01			
DRAWN BY PS	CHECKED BY TAI	PROJ No FE-24-0187	REV U01
ENGINEER YF	SUPERVISOR AK	DRAWING No. 020-0200-LLL-ISO-20545-01	
OPERATIONS	PROJ MGR	SCALE: N.T.S	DATE: 24/06/24