



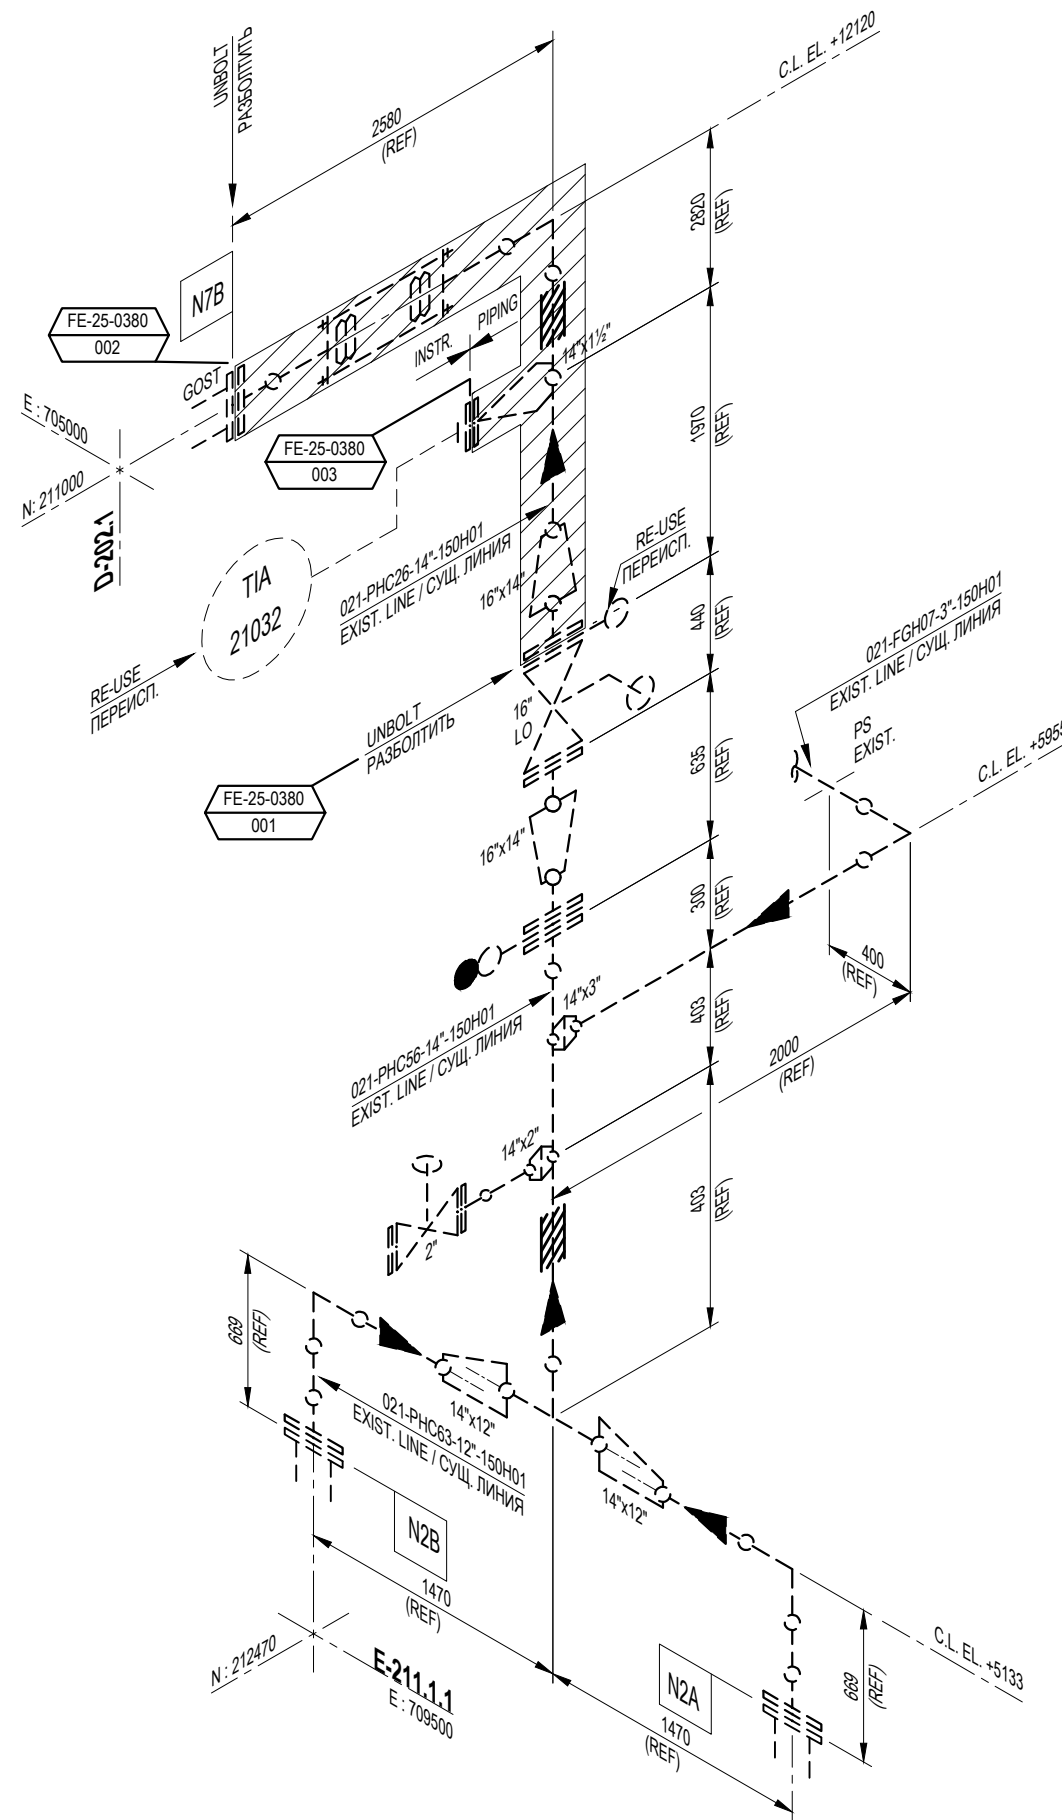

CONSTRUCT DETAILS # 011-0200-LLL-ISO-20262-01
ДЕТАЛИ МОНТАЖА # 011-0200-LLL-ISO-20262-01

WO # 2200623

MOC # 1033298

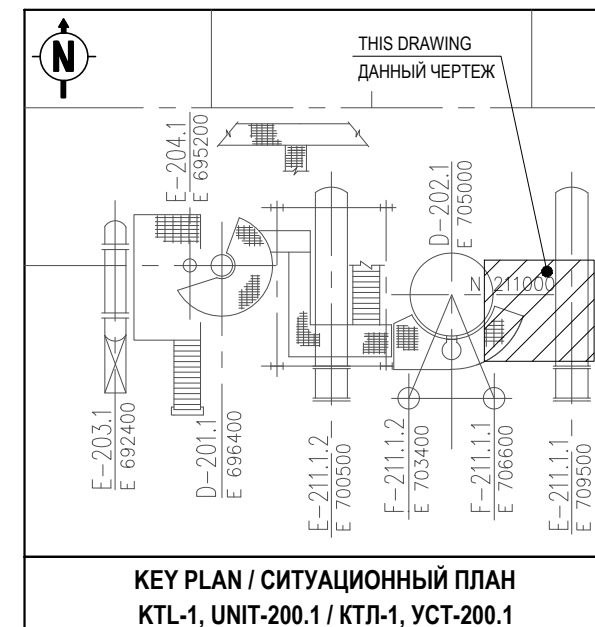

ITEM	QTY	NOM. DIA.	DESCRIPTION
			SHOP MATERIAL
1			
2			
			FIELD MATERIAL
26			
27			
28			
29			
30			
31			
32			
33			
34			
35			
36			
37			
38			
39			
			PIPE SUPPORT
40			
41			
42			
43			
44			

U01	29/01/26	CONSTRUCTION OR USE	AIXN	Y'NYY	BXEX
REV	DATE	REVISION	BY	CHK	ENG



ТЕЇЗШЕВРОЙЛ
TENGZCHEVROIL

TITLE	THE LOOP EXPANSION INSTALLATION PIPING ISOMETRIC 021-PHC26-14"-150H01 УСТАНОВКА ТРУБНОГО КОМПЕНСАТОРА ИЗОМЕТРИЯ ТРУБОПРОВОДА 021-PHC26-14"-150H01
-------	---

NOTES / ПРИМЕЧАНИЯ 1. PID DRG No 1-200_1-B-5006-250380D, 1-200_1-004-250380D СХЕМА ТРУБОПРОВОДОВ И КИП 2. ALL DIMENSIONS SHALL BE FIELD VERIFIED BY CONTRACTOR PRIOR TO DESTRUCT ACTIVITIES. ВСЕ РАЗМЕРЫ ДОЛЖНЫ БЫТЬ ПРОВЕРЕНЫ ПОДРЯДЧИКОМ НА МЕСТЕ ДО ДЕМОНТАЖА.	LINE SPEC. СПЕЦИФИКАЦИЯ ЛИНИИ 150H01	INSULATION / ИЗОЛЯЦИЯ N/A	HYDROTEST ГИДРОИСПЫТАНИЕ N/A	PAINTING / COATING ПОКРАСКА / ПОКРЫТИЕ N/A	PROJ No. FE-25-0380	
	DESIGN PRESSURE РАСЧЕТНОЕ ДАВЛЕНИЕ N/A	OPERATING PRESSURE РАБОЧЕЕ ДАВЛЕНИЕ N/A	NDT/ НЕРАЗРУШ. ИСП. N/A	HARDNESS TEST ИСПЫТАНИЕ НА ТВЕРДОСТЬ N/A	DRAWING No. 011-0200-LLL-ISO-20261-01	REV U01
	DESIGN TEMPERATURE РАСЧЕТНАЯ ТЕМПЕРАТУРА N/A	OPERATING TEMPERATURE РАБОЧЕЕ ТЕМПЕРАТУРА N/A	STRESS RELIEF СНЯТИЕ НАПРЯЖЕНИЙ N/A	WPS# / СВАРОЧНАЯ ПРОЦЕДУРА N/A	SCALE: NTS	DATE: 12/01/26