


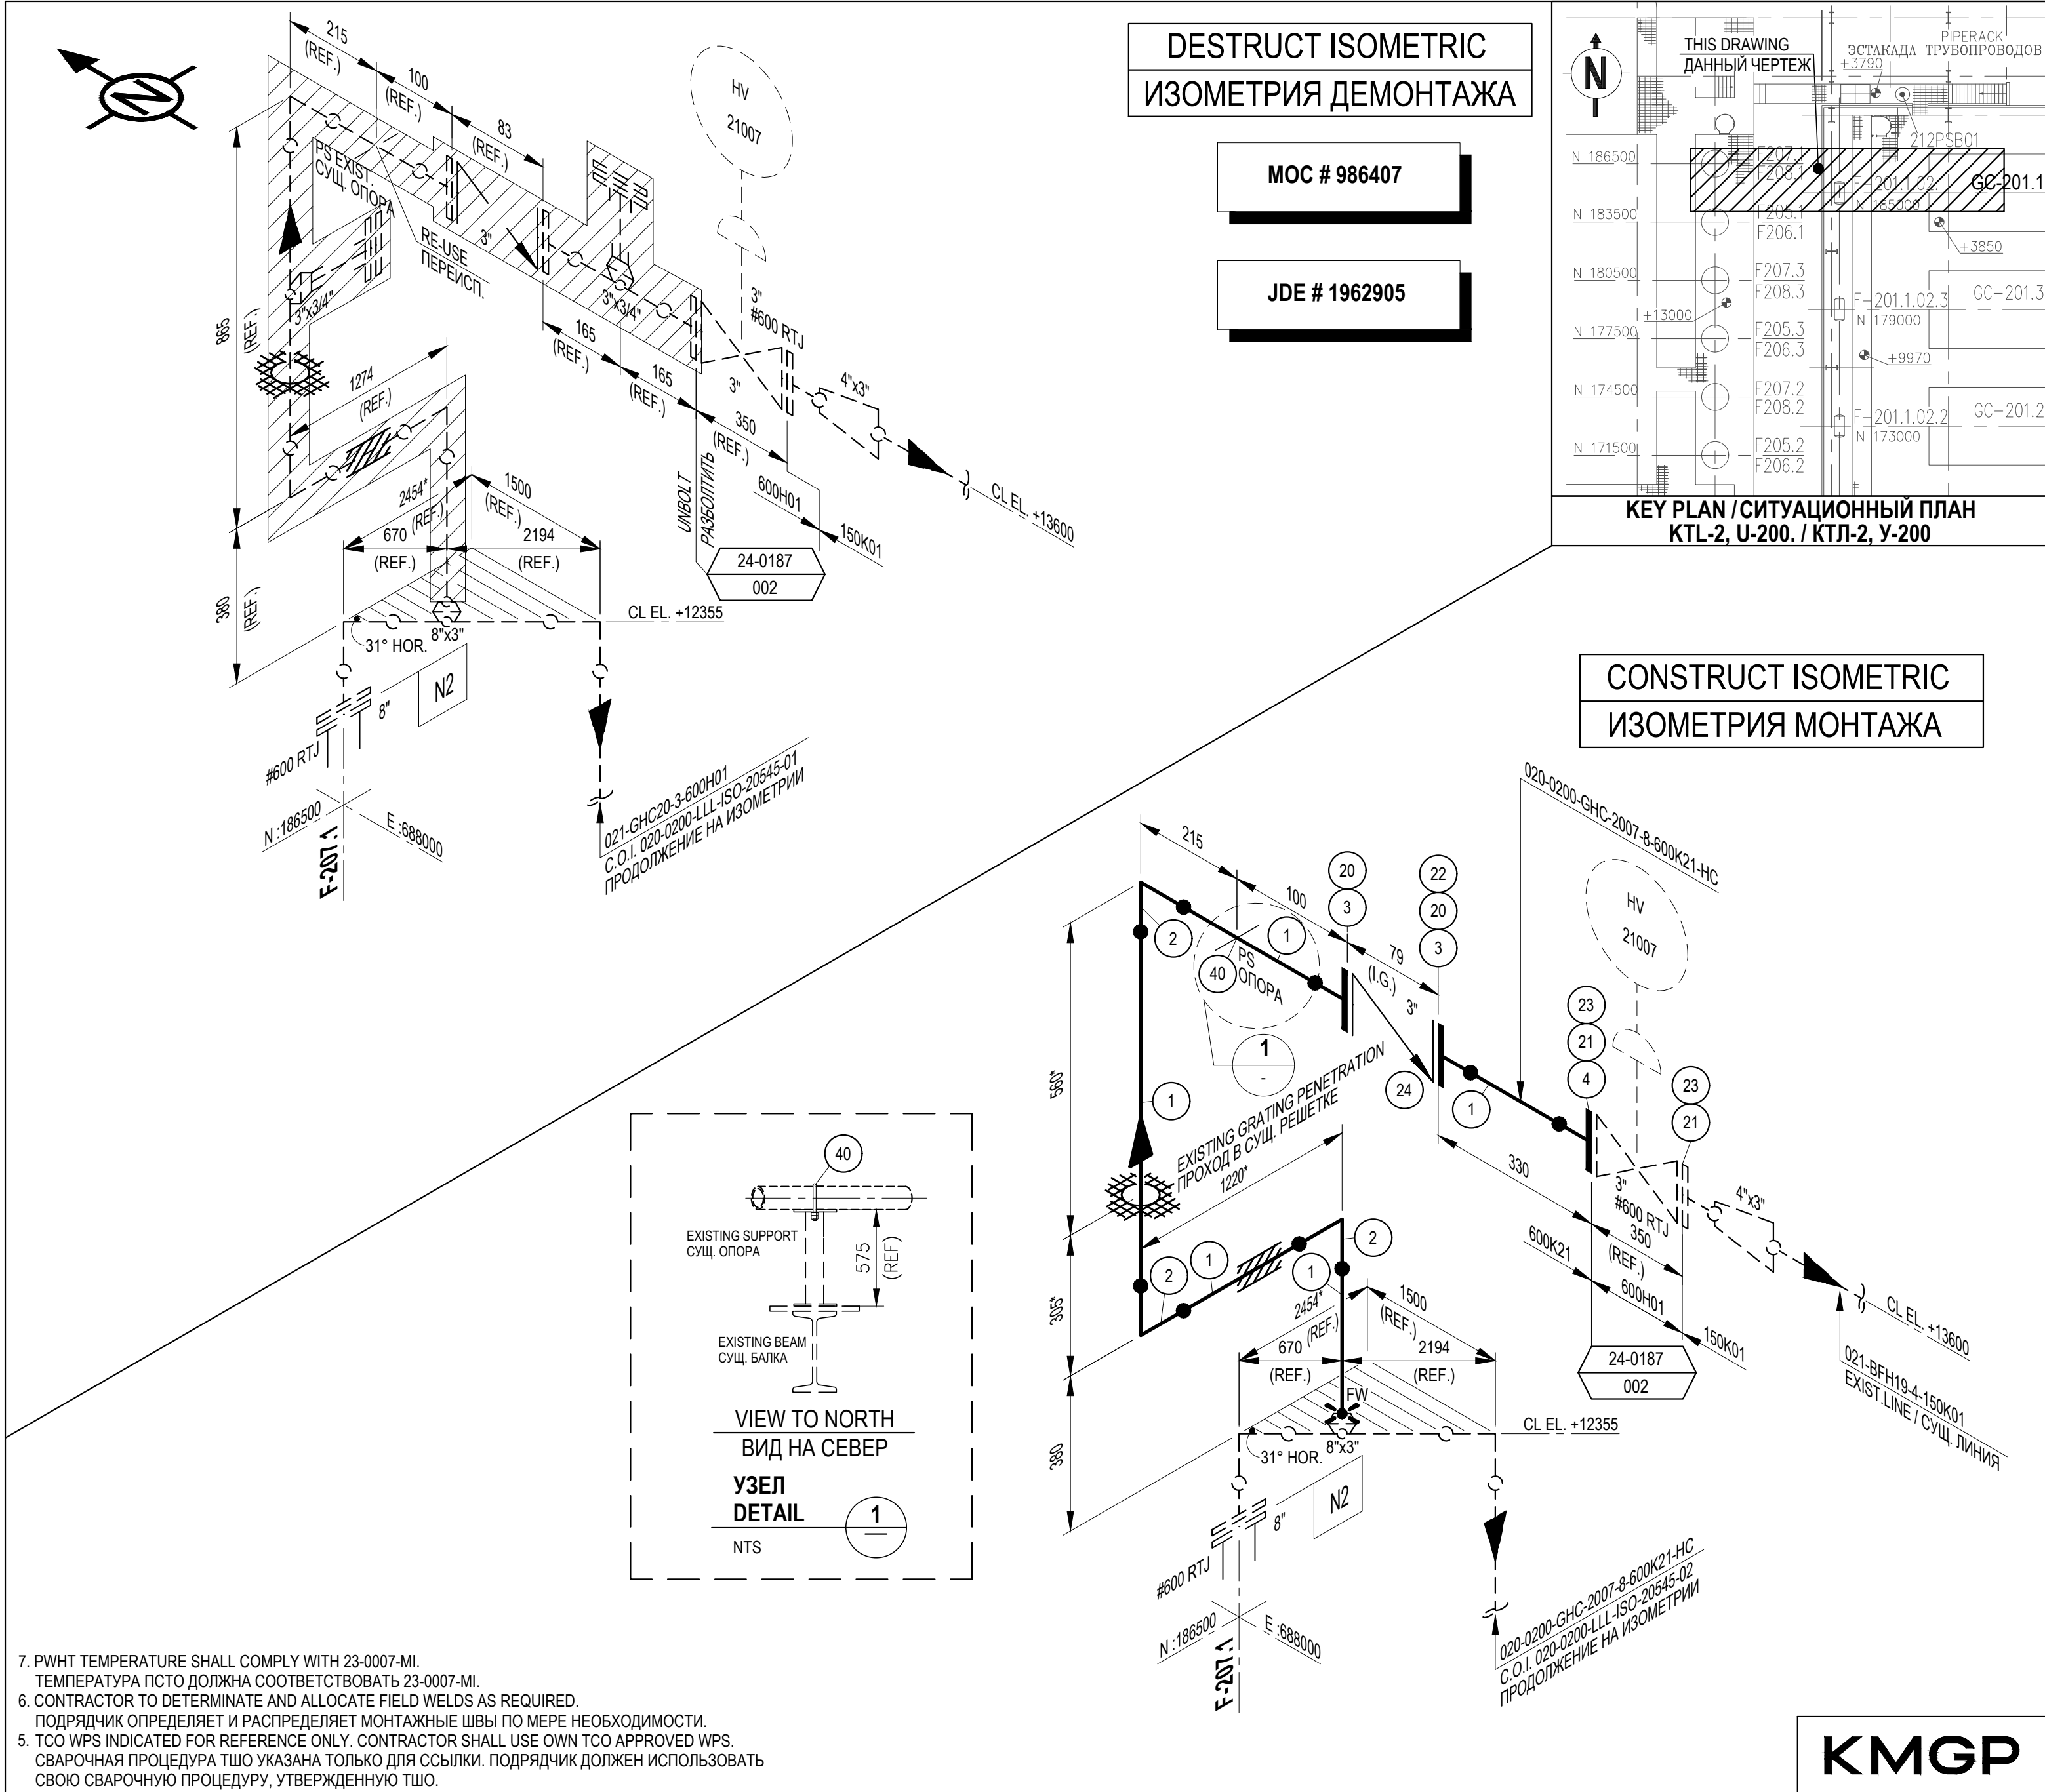

- NOTES / ПРИМЕЧАНИЯ
- PID DRG No 2-200-B-5010-240187D, 2-200-B-5010-240187. СХЕМА ТРУБОПРОВОДОВ И КИП 2-200-B-5010-240187D, 2-200-B-5010-240187.
 - CONTRACTOR TO VERIFY ALL DIMENSIONS AND TIE-IN LOCATIONS PRIOR TO FABRICATION. ПОДРЯДЧИК ОПРЕДЕЛЯЕТ И РАСПРЕДЕЛЯЕТ МОНТАЖНЫЕ ШВЫ ПО МЕРЕ НЕОБХОДИМОСТИ.
 - TSO WPS INDICATED FOR REFERENCE ONLY. CONTRACTOR SHALL USE OWN TSO APPROVED WPS. СВАРОЧНАЯ ПРОЦЕДУРА ТШО УКАЗАНА ТОЛЬКО ДЛЯ ССЫЛКИ. ПОДРЯДЧИК ДОЛЖЕН ИСПОЛЬЗОВАТЬ СВОЮ СВАРОЧНУЮ ПРОЦЕДУРУ, УТВЕРЖДЕННУЮ ТШО.

DESIGN TEMPERATURE РАСЧЕТНАЯ ТЕМПЕРАТУРА		OPERATING TEMPERATURE РАБОЧАЯ ТЕМПЕРАТУРА		HYDROTEST ГИДРОИСПЫТАНИЕ		PAINTING / COATING ПОКРАСКА / ПОКРЫТИЕ		DRAWN BY PS		CHECKED BY TAI		PROJ No FE-24-0187		REV U01	
DESIGN PRESSURE РАСЧЕТНОЕ ДАВЛЕНИЕ		OPERATING PRESSURE РАБОЧЕЕ ДАВЛЕНИЕ		NDT/ НЕРАЗРУШ. ИСП.		HARDNESS TEST ИСПЫТАНИЕ НА ТВЕРДОСТЬ		ENGINEER YF		SUPERVISOR AK		DRAWING No. 020-0200-LLL-ISO-20545-03			
LINE SPEC. СПЕЦИФИКАЦИЯ ЛИНИИ		INSULATION / ИЗОЛЯЦИЯ		VT-100%, RT/PAUT-100%, MT-100%		STRESS RELIEF СНЯТИЕ НАПРЯЖЕНИЙ		OPERATIONS		PROJ MGR		SCALE: N.T.S		DATE: 25/06/24	
600K21		3" - 40MM HC		120barg		200HB									
80barg		22.5barg		NOTE 7 ПРИМ. 7 YES		WPS# / СВАРОЧНАЯ ПРОЦЕДУРА NOTE 5 ПРИМ. 5									
80°C		47°C				20PW									

ITEM	QTY	NOM. DIA.	DESCRIPTION
SHOP MATERIAL			
1	3M	3"	PIPE SCH XS SMLS LTCS A333 GR.6 BE
2	3	3"	ELL BW 90 DEG LR SCH XS LTCS A420 WPL6
3	2	3"	FLG WN 600# RF LTCS A350 LF2 CL.1 SCH XS
4	1	3"	FLG WN 600# RTJ LTCS A350 LF2 CL.1 SCH XS (OUT OF SPEC)
5			
6			
7			
8			
9			
10			
11			
12			
13			
14			
15			
16			
17			
18			
19			
FIELD MATERIALS			
20	2	3"	GASKET 600# 316SS SP WND GRAPHITE IR
21	2	3"	GASKET 600# RTJ SS OCTAGONAL RING R31
22	8	M20	x 210 STUD-BOLT A320 GR L7M/A194 GR 7M (S3) WITH 2 NUTS
23	16	M20	x 140 STUD-BOLT A320 GR L7M/A194 GR 7M (S3) WITH 2 NUTS
24	1	3"	CHECK DUAL WAFER LUG 600# RF LTCS A352 LCC TRIM 16 THROU BOLTED
25			
26			
27			
28			
29			
30			
31			
32			
33			
34			
35			
36			
37			
38			
39			
PIPE SUPPORT			
40	1	3"	U-BOLT, TYPE - ANCHOR, FIG. 283, CS, PIPE SIZE - 3" (CARPENTER AND PATERSON LTD)
41			
42			
43			
44			
U01	26/12/24	CONSTRUCTION OR USE	TAI YF ALT
REV	DATE	REVISION	BY CHK ENG



ТЕНІЗШЕВРОЙЛ

TENGIZCHEVROIL

TITLE

KTL-2 F-207.1 SWEET GAS LINE REPLACEMENT PIPING ISOMETRIC 020-0200-GHC-2007-8"-600K21-HC

КТЛ-2 F-207.1 ЗАМЕНА ЛИНИИ КИСЛОГО ГАЗА ИЗОМЕТРИЯ ТРУБОПРОВОДА 020-0200-GHC-2007-8"-600K21-HC

KMGP