
A2 ISO BORDER

020-0900-LLL-ISO-20029-01

CONSTRUCT DETAIL
ДЕТАЛЬ МОНТАЖА

DESTRUCT DETAILS # 020-0900-LLL-ISO-20028-01
ДЕТАЛИ ДЕМОНТАЖА # 020-0900-LLL-ISO-20028-01

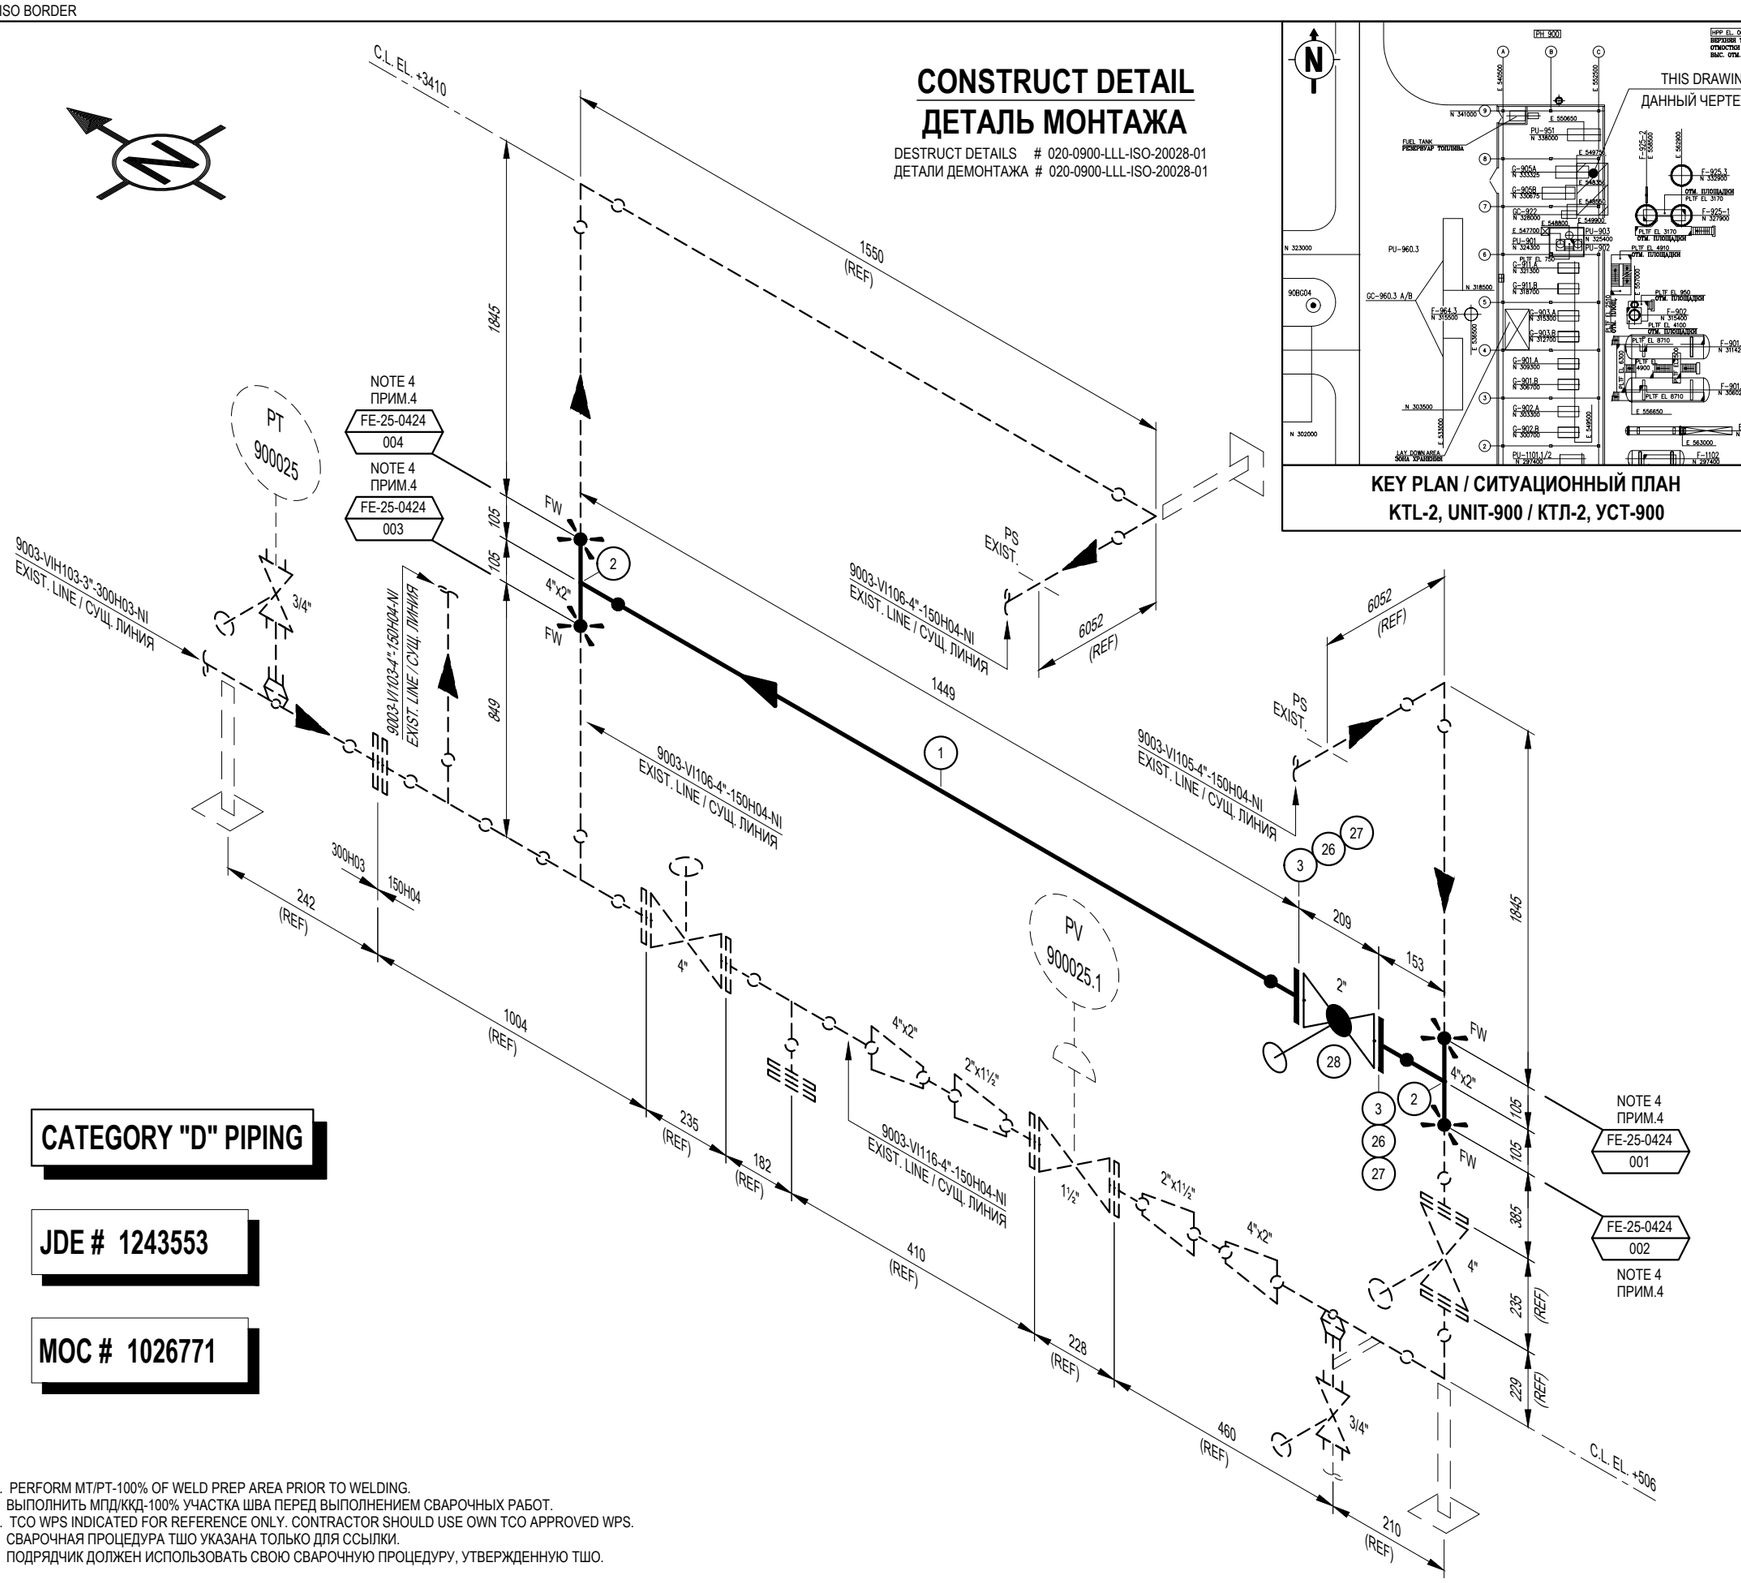

KEY PLAN / СИТУАЦИОННЫЙ ПЛАН
KTL-2, UNIT-900 / КТЛ-2, УСТ-900

ITEM	QTY	NOM. DIA.	DESCRIPTION
			SHOP MATERIAL
1	1.5 M	2"	PIPE SCH XS SMLS LTCS A333 GR.6 BE
2	2	4"	x 2" TEE RED BW SCH STD/XS LTCS A420 WPL6
3	2	2"	FLG WN 150# RF LTCS A350 LF2 CL.1 SCH XS
4			
5			
			FIELD MATERIAL
26	2	2"	GASKET 150# 316SS SPIRAL WOUND GRAPHITE IR
27	8	M16	x 90 STUD-BOLT A320 GR L7M/A194 GR 7M (S3) WITH 2 NUTS
28	1	2"	GLOBE 150# RF LTCS A352 LCC TRIM 16 OS&Y HW
29			
30			
31			
32			
33			
34			
35			
36			
37			
38			
39			
			PIPE SUPPORT
40			
41			
42			
43			
44			

REV	DATE	REVISION	BY	CH'K	ENG
U01	18/11/25	TCO REVIEW	ZBAS	ZBAS	XQTO

CATEGORY "D" PIPING

JDE # 1243553

MOC # 1026771

4. PERFORM MT/PT-100% OF WELD PREP AREA PRIOR TO WELDING.
 ВЫПОЛНИТЬ МПД/ККД-100% УЧАСТКА ШВА ПЕРЕД ВЫПОЛНЕНИЕМ СВАРОЧНЫХ РАБОТ.
5. TCO WPS INDICATED FOR REFERENCE ONLY. CONTRACTOR SHOULD USE OWN TCO APPROVED WPS.
 СВАРОЧНАЯ ПРОЦЕДУРА ТШО УКАЗАНА ТОЛЬКО ДЛЯ ССЫЛКИ.
 ПОДРЯДЧИК ДОЛЖЕН ИСПОЛЬЗОВАТЬ СВОЮ СВАРОЧНУЮ ПРОЦЕДУРУ, УТВЕРЖДЕННУЮ ТШО.

NOTES / ПРИМЕЧАНИЯ

1. PID DRG No 2-900_3-B-3220-250424.
 СХЕМА ТРУБОПРОВОДОВ И КИП
2. ALL DIMENSIONS SHALL BE FIELD VERIFIED BY CONTRACTOR PRIOR TO DESTRUCT ACTIVITIES.
 ВСЕ РАЗМЕРЫ ДОЛЖНЫ БЫТЬ ПРОВЕРЕНЫ ПОДРЯДЧИКОМ НА МЕСТЕ ДО ДЕМОНТАЖА.
3. TES L-ST-2056 LINE CLASS 150H21 MATERIAL USED LIEU TO LEGACY LINE CLASS 150H04 MATERIAL.
 МАТЕРИАЛ TES L-ST-2056 КЛАСС ЛИНИИ 150H21 ИСПОЛЬЗОВАН ВМЕСТО МАТЕРИАЛА КЛАССА ЛИНИИ 150H04.

LINE SPEC. / СПЕЦИФИКАЦИЯ ЛИНИИ: NOTE 3 / 150H04	INSULATION / ИЗОЛЯЦИЯ: N/A	HYDROTEST / ГИДРОИСПЫТАНИЕ: SERVICE TEST	PAINTING / COATING / ПОКРАСКА / ПОКРЫТИЕ: 3.2		
DESIGN PRESSURE / РАСЧЕТНОЕ ДАВЛЕНИЕ: 7 barg	OPERATING PRESSURE / РАБОЧЕЕ ДАВЛЕНИЕ: 5 barg	NDT/ НЕРАЗРУШ. ИСП.: VISUAL-100%	HARDNESS TEST / ИСПЫТАНИЕ НА ТВЕРДОСТЬ: N/A		
DESIGN TEMPERATURE / РАСЧЕТНАЯ ТЕМПЕРАТУРА: 75 °C	OPERATING TEMPERATURE / РАБОЧАЯ ТЕМПЕРАТУРА: 55 °C	STRESS RELIEF / СНЯТИЕ НАПРЯЖЕНИЙ: N/A	WPS# / СВАРОЧНАЯ ПРОЦЕДУРА: 20AW NOTE 5		

ТЕҢІЗШЕВРОЙЛ
TENGIZCHEVROIL

TITLE

REPLACE BYPASS VALVE 23-0900-PV-900025.1
PIPING ISOMETRIC
9003-VI106-4"-150H04-NI

ЗАМЕНА БАЙПАС КЛАПАН 23-0900-PV-900025.1
ИЗОМЕТРИЯ ТРУБОПРОВОДА
9003-VI106-4"-150H04-NI

PROJ No. **FE-25-0424**

DRAWING No. **020-0900-LLL-ISO-20029-01**

REV **U01**

SCALE: NTS

DATE: 11/11/25

THIS DRAWING AND THE DESIGN IT COVERS ARE THE PROPERTY OF TENGIZCHEVROIL THEY ARE MERELY LOANED AND ON THE BORROWERS EXPRESS AGREEMENT THAT THEY WILL NOT BE REPRODUCED COPIED LOANED EXHIBITED NOR USED EXCEPT IN THE LIMITED WAY AND PRIVATE USE PERMITTED AND WRITTEN CONSENT GIVEN BY TENGIZCHEVROIL TO THE BORROWER.